CONCEPT PLAN SET

SINGLE STOREY, 4 BEDROOM


756 Quia Road Gunnedah NSW
Lot 3 DP 263990

Client: A Sample Client
Council: Gunnedah Shire
Zone: RU1 Primary Production
Site area: 50.93 ha
Issue: Concept, revision A, 11/11/2026

DRAWING LIST

DRAWING NUMBER	TITLE	SCALE
GI-L3DP263990-A-001	Cover sheet and drawing list	AS SHOWN
GI-L3DP263990-A-002	Site plan	1:500 @ A3
GI-L3DP263990-A-003	Ground floor plan	1:150 @ A3
GI-L3DP263990-A-004	Roof plan	1:150 @ A3
GI-L3DP263990-A-005	Elevations	1:150 @ A3
GI-L3DP263990-A-006	Section	1:100 @ A3
GI-L3DP263990-A-007	Site analysis and setbacks	1:10000 @ A3
GI-L3DP263990-A-008	Schedules	NTS

LOCALITY

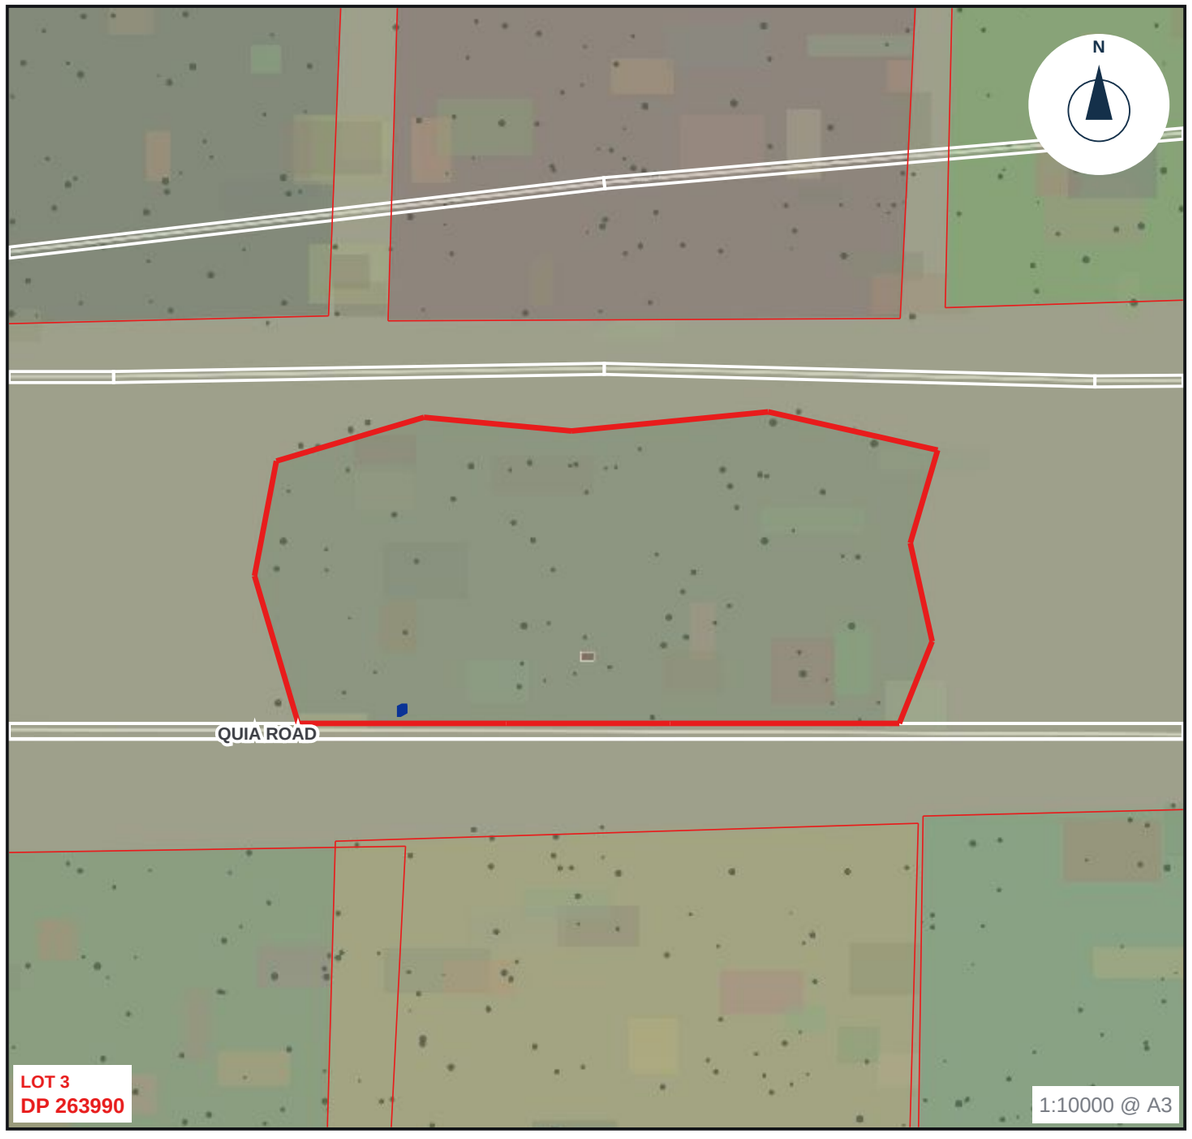

This is a concept design for discussion. Setbacks, levels and boundaries are indicative and have not been checked by a surveyor, certifier or council. Where a council rule is marked check with council it has not been confirmed.

Prepared with Glide Inside

Sample Builder Homes

Prepared with Glide Inside
Glide Inside

PROJECT
SINGLE STOREY, 4 BEDROOM
756 QUIA ROAD GUNNEDAH NSW
LOT 3 DP 263990

CLIENT
A Sample Client

DRAWING TITLE
COVER SHEET AND DRAWING LIST


REV	DATE	DESCRIPTION	DRN	CHK	APP
A	11/11/2026	Concept			

NOT CHECKED. NOT APPROVED.

DRAWING NUMBER: **GI-L3DP263990-A-001**
REV: **A**
STATUS: **CONCEPT**
DATE: **11/11/2026**
DRAWN:
CHECKED:
APPROVED:
JOB NO.:
SCALE: **AS SHOWN**
SHEET: **1 OF 8**
SIZE: **A3**

CONCEPT ONLY. TO BE VERIFIED BY A SUITABLY QUALIFIED PERSON BEFORE ANY USE FOR APPROVAL OR CONSTRUCTION. Not a survey. Not a development application drawing.
Cadastre, imagery and contours: NSW Spatial Services (CC BY). Aerial underlay: NSW Spatial Services (c) Department of Customer Service 2020. Sample picture only. Reduced resolution, not for measurement.

SITE PLAN 1:500 @ A3

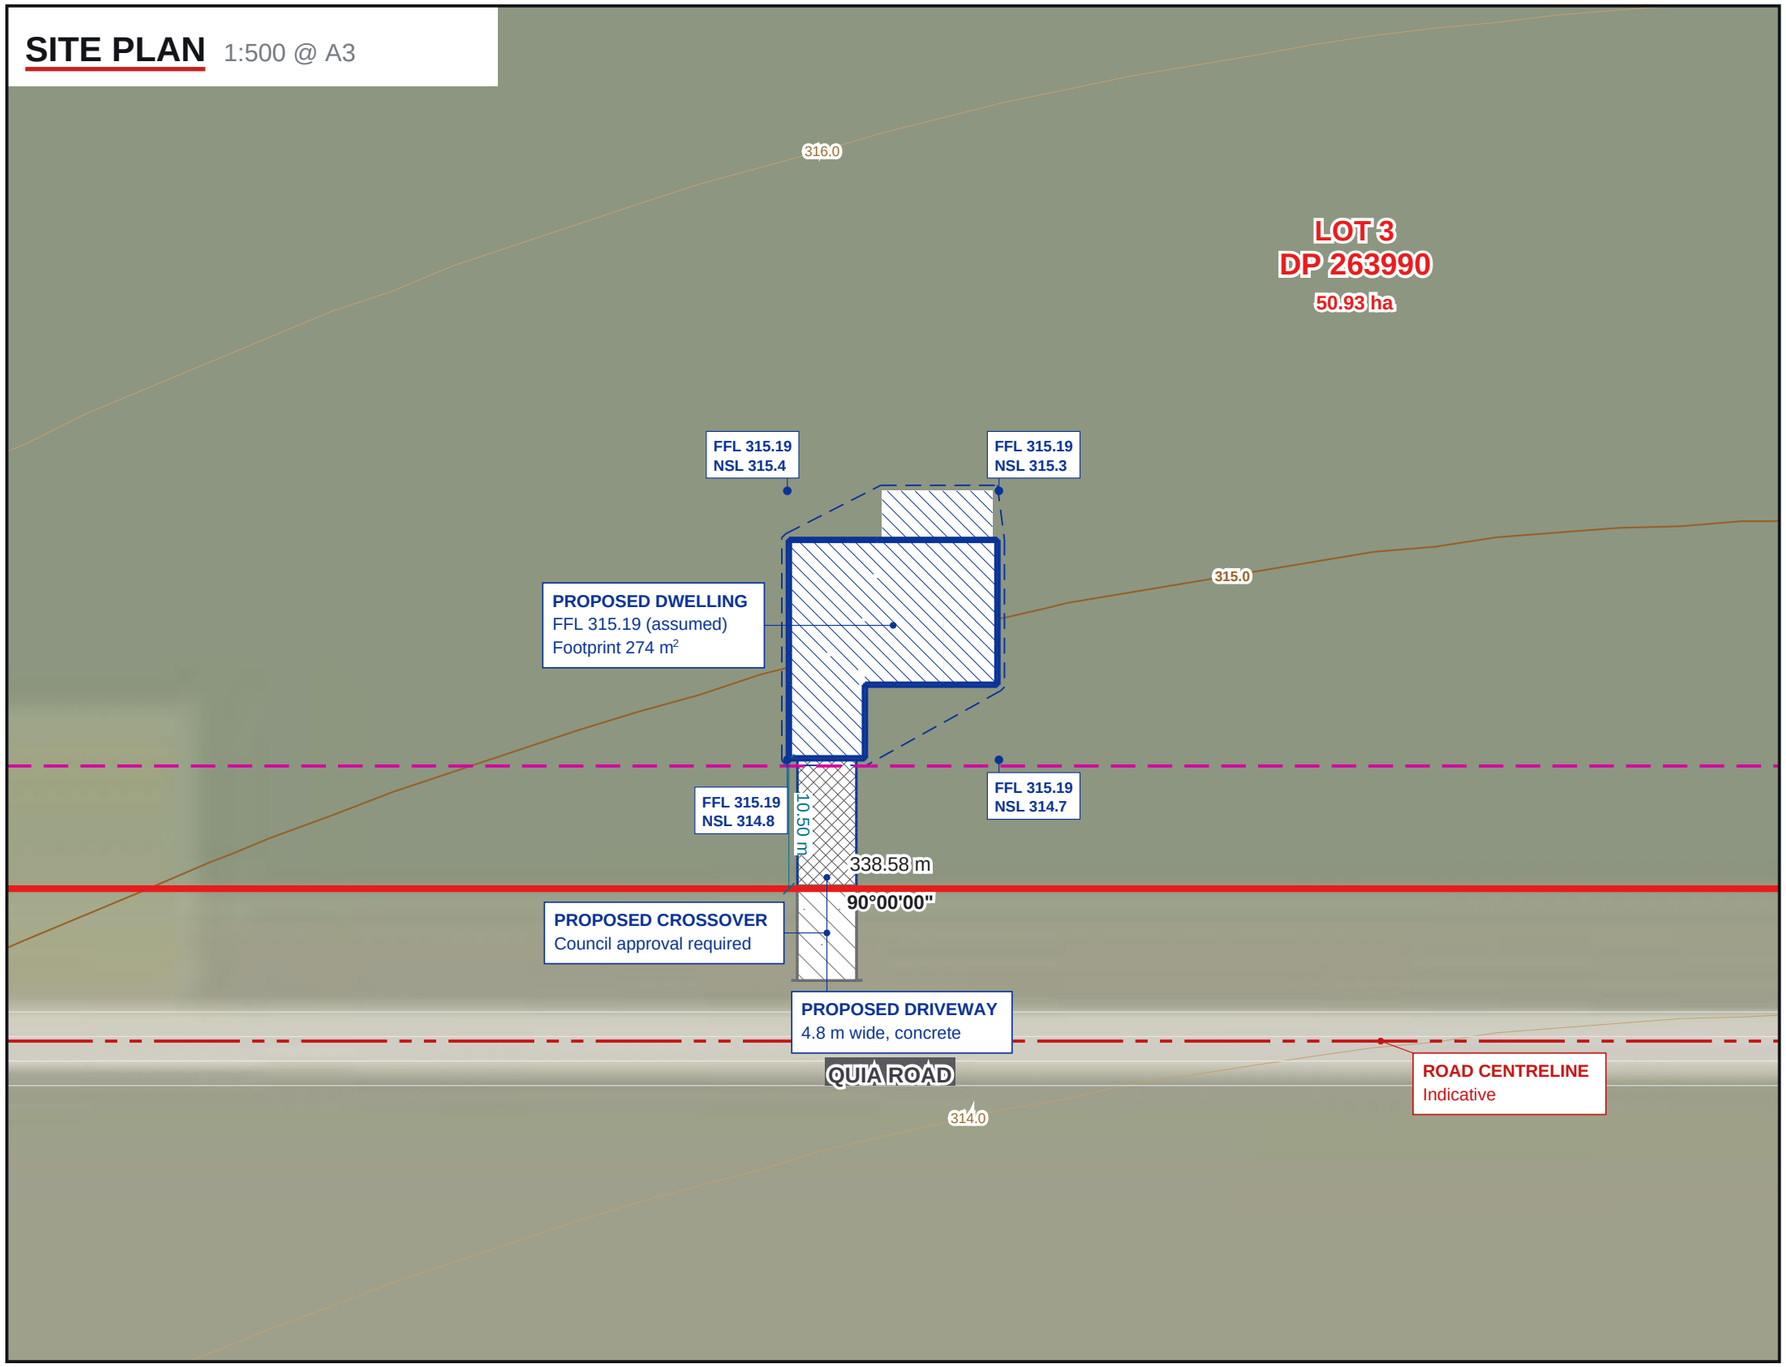

N


SCALE 1:500 @ A3

North is MGA grid north.

Plan up is north.

0 5 10 15 20 m

KEY PLAN

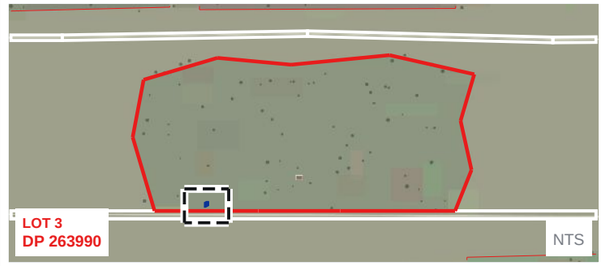

LEGEND

- Lot boundary (existing)
- Neighbouring lots (cadastre)
- Indicative setback envelope
- Road centreline (phantom, indicative)
- Contour (minor, major)
- Dimension to boundary
- Proposed works
- Hardstand (driveway)
- Concrete (crossover)
- Road pavement

NOTES

1. Concept only. To be verified by a suitably qualified person before any use for approval or construction.
2. Boundaries are from the cadastre, are indicative only, and are not a survey. A registered survey is required.
3. Large lot: this sheet shows the house and its surrounds. The whole lot is shown on the key plan, with the area covered by this sheet outlined.
4. The aerial underlay is reduced in resolution and is for orientation only. It is not for measurement. Cadastre drawn in red over the aerial.
5. Setbacks are indicative (Gunnedah Shire Council). The sources, the figures provided and the items to confirm are on sheet 7. A figure marked check with council is not confirmed.
6. Levels are indicative only, from the NSW 5 m DEM, and are not survey. Contours are at 1.0 m intervals and spot levels are to 0.1 m. A registered survey is required.
7. FFL 315.19 m AHD is assumed from the ground level at the house, not designed. NSL is the natural surface level from the terrain model at each house corner.
8. FFL is below the natural surface at one or more house corners. Cut is required at those corners: refer to site works.

Sample Builder Homes

Prepared with Glide Inside

Glide Inside

PROJECT

SINGLE STOREY, 4 BEDROOM

756 QUIA ROAD GUNNEDAH NSW

LOT 3 DP 263990

CLIENT

A Sample Client

DRAWING TITLE

SITE PLAN

REV	DATE	DESCRIPTION	DRN	CHK	APP
A	11/11/2026	Concept			

NOT CHECKED. NOT APPROVED.

DRAWING NUMBER	REV	STATUS
GI-L3DP263990-A-002	A	CONCEPT

DATE	DRAWN	CHECKED	APPROVED	JOB NO.
11/11/2026				


SCALE	SHEET	SIZE
1:500 @ A3	2 OF 8	A3

CONCEPT ONLY. TO BE VERIFIED BY A SUITABLY QUALIFIED PERSON BEFORE ANY USE FOR APPROVAL OR CONSTRUCTION. Not a survey. Not a development application drawing.

Cadastre, imagery and contours: NSW Spatial Services (CC BY). Aerial underlay: NSW Spatial Services (c) Department of Customer Service 2020. Sample picture only. Reduced resolution, not for measurement.

NOTES

1. Dimensions are in millimetres, between wall faces as drawn. Wall construction is not designed here.
2. Floor level of this storey: RL 315.19 m AHD (assumed from the ground level at the house).
3. Ceiling height 2.55 m.
4. Section A-A is cut where the red chain line crosses the plan: see sheet 6.
5. Furniture is indicative and is not part of the design.

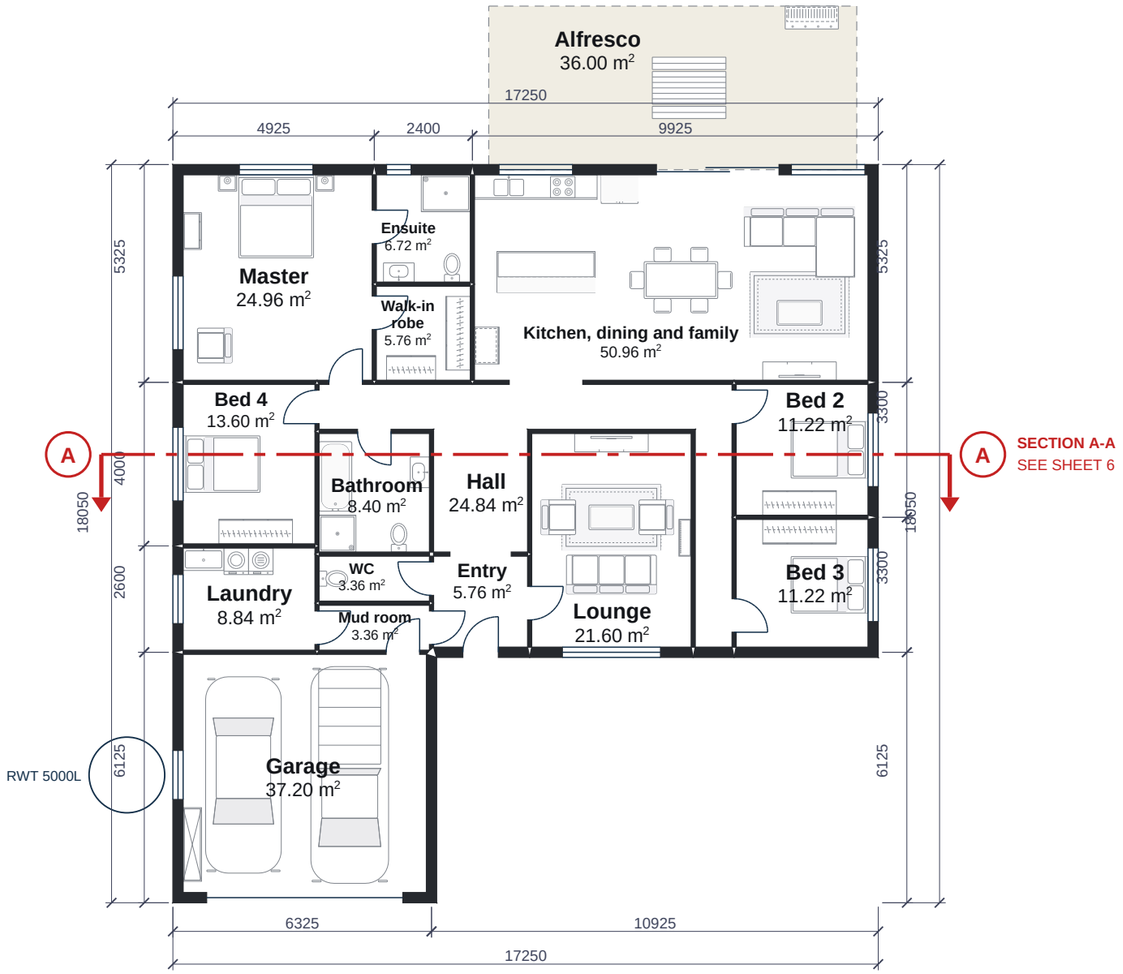

GROUND FLOOR PLAN

1:150 @ A3

0 2 4 6 8 10 m

N


Sample Builder Homes	PROJECT **SINGLE STOREY, 4 BEDROOM** 756 QUIA ROAD GUNNEDAH NSW LOT 3 DP 263990	REV	DATE	DESCRIPTION	DRN	CHK	APP	DRAWING NUMBER **GI-L3DP263990-A-003**
	CLIENT **A Sample Client**	A	11/11/2026	Concept				REV **A**
Prepared with Glide Inside Glide Inside	DRAWING TITLE **GROUND FLOOR PLAN**	NOT CHECKED. NOT APPROVED.						STATUS **CONCEPT**

DATE	DRAWN	CHECKED	APPROVED	JOB NO.
11/11/2026				

SCALE	SHEET	SIZE
1:150 @ A3	**3 OF 8**	**A3**

CONCEPT ONLY. TO BE VERIFIED BY A SUITABLY QUALIFIED PERSON BEFORE ANY USE FOR APPROVAL OR CONSTRUCTION. Not a survey. Not a development application drawing.
Cadastre, imagery and contours: NSW Spatial Services (CC BY). Aerial underlay: NSW Spatial Services (c) Department of Customer Service 2020. Sample picture only. Reduced resolution, not for measurement.

ROOF PLAN 1:150 @ A3

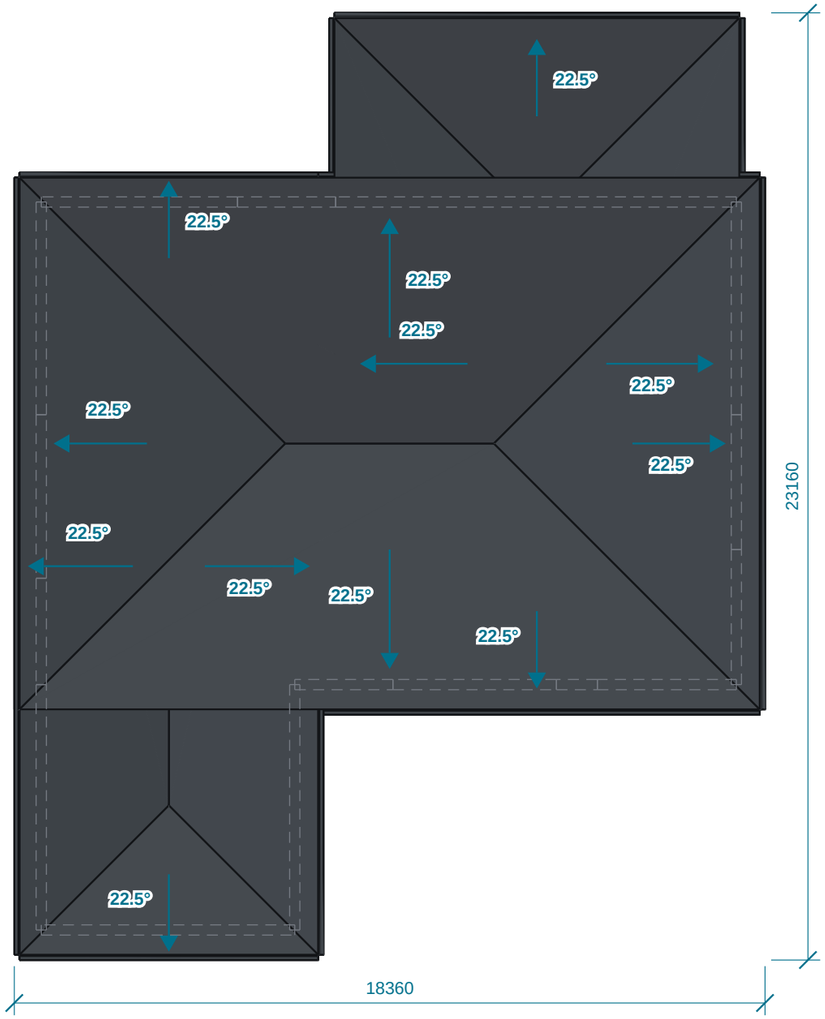

0 2 4 6 8 10 m

ROOF DATA

Roof form	**Hip roof**
Pitch	**22.5°**
Eaves overhang	**450 mm**
Roof area (sloped)	**684 m²**
Roof sheeting	**Not stated**
Highest point	**5.08 m above FFL, RL 320.27**
Above natural surface	**5.6 m at the lowest house corner**

LEGEND

- Ridge, hip and valley
- Direction of fall, with pitch
- Exterior walls below

Roof geometry is taken from the same model as the 3D view. Sheeting, gutters, downpipes, battens and roof framing are not designed here and are to be confirmed by the builder and a structural engineer. Dimensions are in millimetres.

Sample Builder Homes

Prepared with Glide Inside

PROJECT
SINGLE STOREY, 4 BEDROOM
756 QUIA ROAD GUNNEDAH NSW
LOT 3 DP 263990

CLIENT
A Sample Client


DRAWING TITLE
ROOF PLAN

REV	DATE	DESCRIPTION	DRN	CHK	APP
A	11/11/2026	Concept			

NOT CHECKED. NOT APPROVED.

DRAWING NUMBER **GI-L3DP263990-A-004**
REV **A**
STATUS **CONCEPT**
DATE **11/11/2026**
DRAWN
CHECKED
APPROVED
JOB NO.
SCALE **1:150 @ A3**
SHEET **4 OF 8**
SIZE **A3**


CONCEPT ONLY. TO BE VERIFIED BY A SUITABLY QUALIFIED PERSON BEFORE ANY USE FOR APPROVAL OR CONSTRUCTION. Not a survey. Not a development application drawing.
Cadastre, imagery and contours: NSW Spatial Services (CC BY). Aerial underlay: NSW Spatial Services (c) Department of Customer Service 2020. Sample picture only. Reduced resolution, not for measurement.

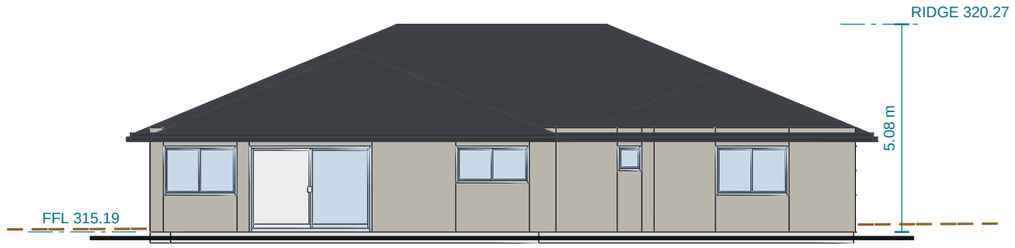

NORTH ELEVATION 1:150 @ A3



EAST ELEVATION 1:150 @ A3

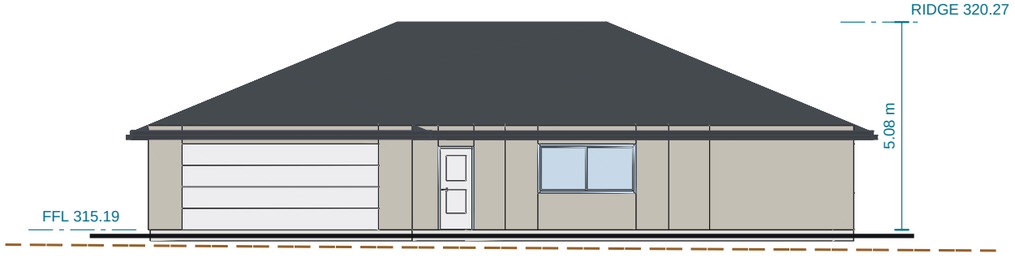

SOUTH ELEVATION 1:150 @ A3



WEST ELEVATION 1:150 @ A3

Sample Builder Homes

Prepared with Glide Inside

PROJECT
SINGLE STOREY, 4 BEDROOM
756 QUIA ROAD GUNNEDAH NSW
LOT 3 DP 263990

CLIENT
A Sample Client

DRAWING TITLE
ELEVATIONS

REV	DATE	DESCRIPTION	DRN	CHK	APP
A	11/11/2026	Concept			


NOT CHECKED. NOT APPROVED.

DRAWING NUMBER: **GI-L3DP263990-A-005**
REV: **A**
STATUS: **CONCEPT**
DATE: **11/11/2026**
DRAWN:
CHECKED:
APPROVED:
JOB NO.:
SCALE: **1:150 @ A3**
SHEET: **5 OF 8**
SIZE: **A3**

CONCEPT ONLY. TO BE VERIFIED BY A SUITABLY QUALIFIED PERSON BEFORE ANY USE FOR APPROVAL OR CONSTRUCTION. Not a survey. Not a development application drawing.
Cadastre, imagery and contours: NSW Spatial Services (CC BY). Aerial underlay: NSW Spatial Services (c) Department of Customer Service 2020. Sample picture only. Reduced resolution, not for measurement.

SECTION A-A 1:100 @ A3

Cut across the centre of the house, looking south. Cut walls are hatched, slabs solid. The section line is marked on the floor plans.

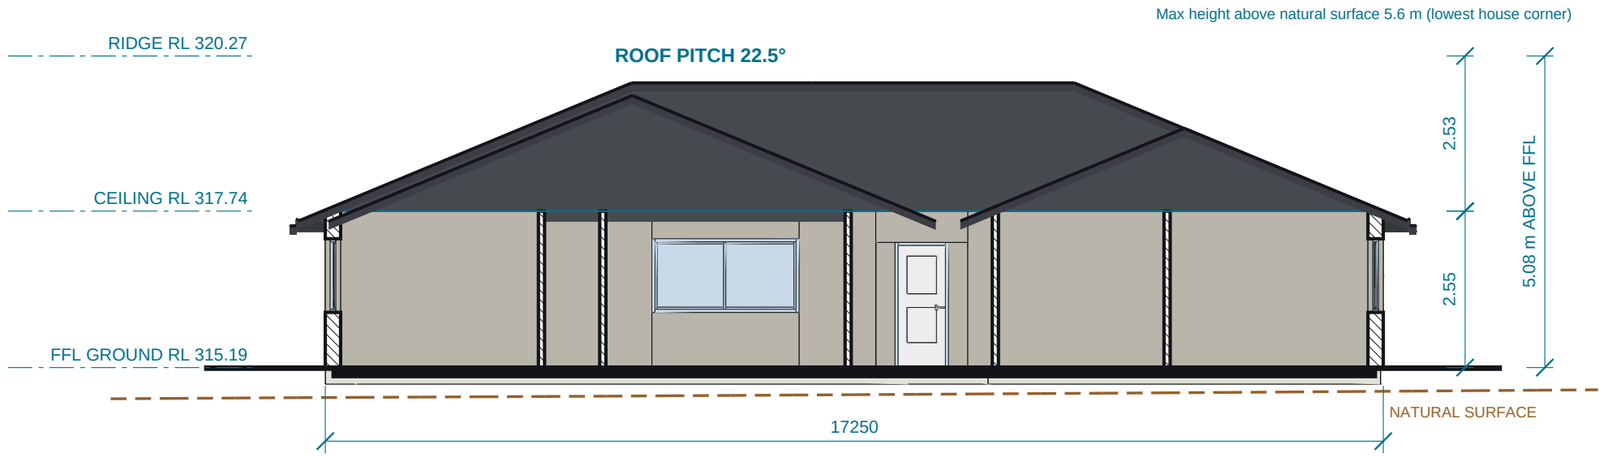



Sample Builder Homes

Prepared with Glide Inside

PROJECT
SINGLE STOREY, 4 BEDROOM
756 QUIA ROAD GUNNEDAH NSW
LOT 3 DP 263990

CLIENT
A Sample Client

DRAWING TITLE
SECTION


REV	DATE	DESCRIPTION	DRN	CHK	APP
A	11/11/2026	Concept			

NOT CHECKED. NOT APPROVED.

DRAWING NUMBER: **GI-L3DP263990-A-006**
REV: **A**
STATUS: **CONCEPT**
DATE: **11/11/2026**
DRAWN:
CHECKED:
APPROVED:
JOB NO.:
SCALE: **1:100 @ A3**
SHEET: **6 OF 8**
SIZE: **A3**

CONCEPT ONLY. TO BE VERIFIED BY A SUITABLY QUALIFIED PERSON BEFORE ANY USE FOR APPROVAL OR CONSTRUCTION. Not a survey. Not a development application drawing.
Cadastre, imagery and contours: NSW Spatial Services (CC BY). Aerial underlay: NSW Spatial Services (c) Department of Customer Service 2020. Sample picture only. Reduced resolution, not for measurement.

SITE ANALYSIS 1:10000 @ A3

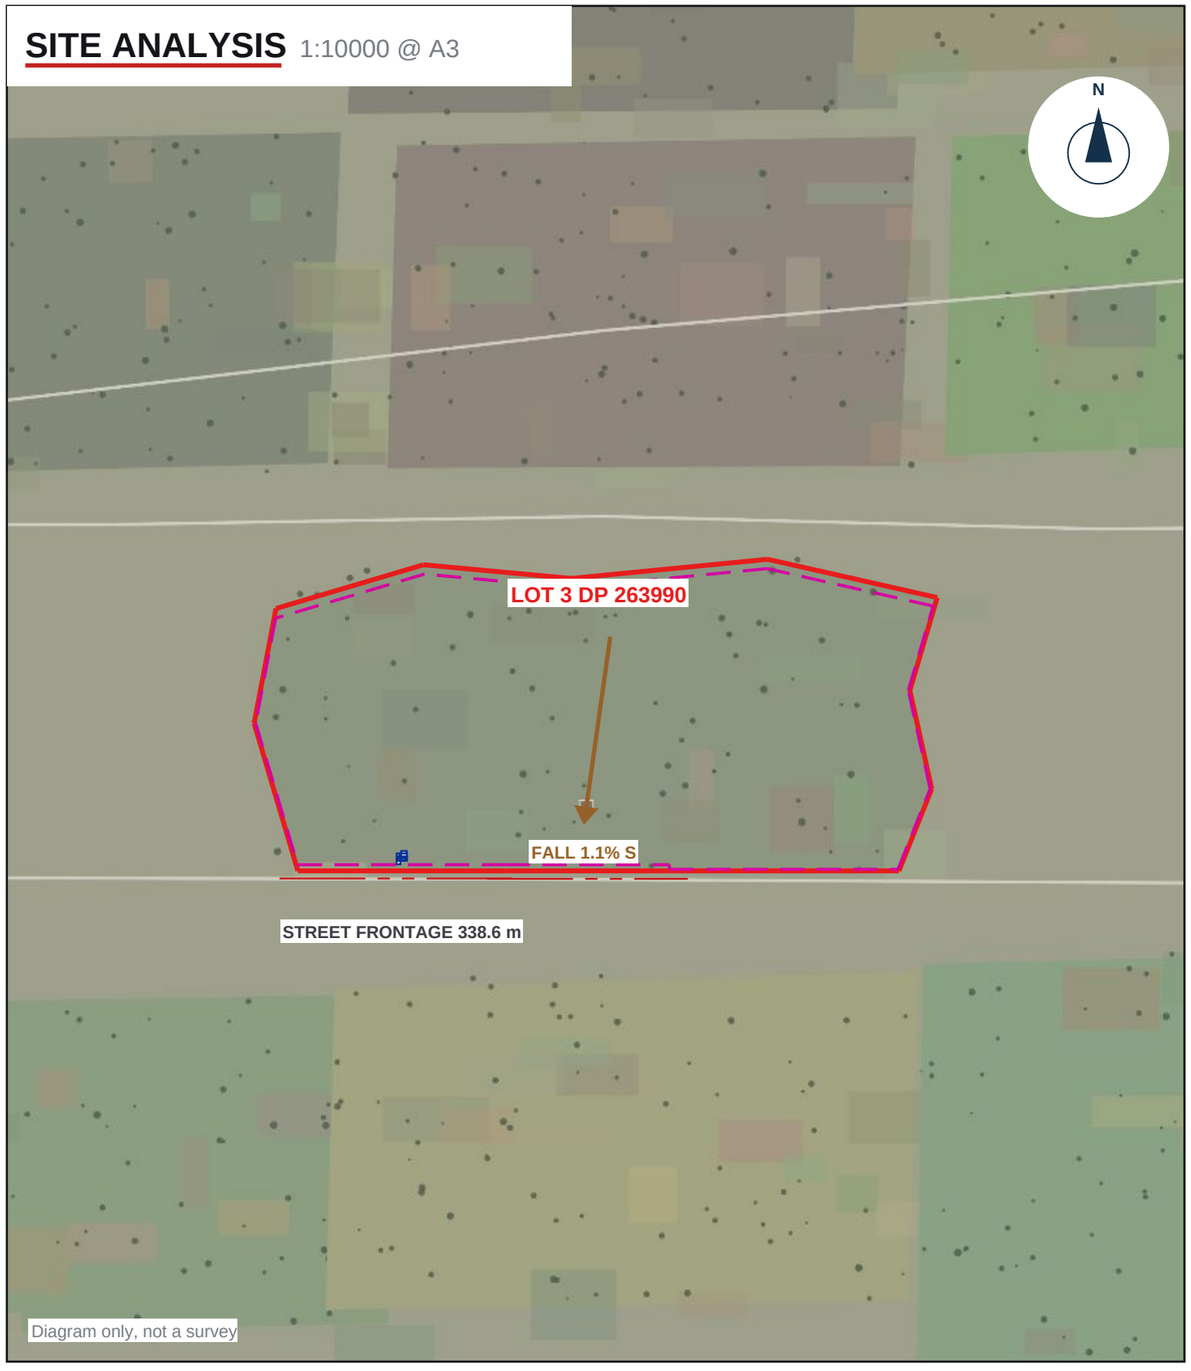

SITE FACTS

ITEM	DETAIL
Address	756 Quia Road Gunnedah NSW
Lot and DP	LOT 3 DP 263990
Council	Gunnedah Shire
Zone	RU1 Primary Production
Site area	50.93 ha (registered)
Frontage and depth	338.6 m by 507.9 m
Corner lot	No
Ground fall	6.66 m across the lot, 1.1% towards the S
Floor level	FFL 315.19 m AHD (assumed)
Overlays	Bushfire, flood, heritage and easements not checked

SETBACKS: REQUIRED AND PROVIDED

BOUNDARY	REQUIRED	PROVIDED	RESULT	SOURCE AND CHECK
Front boundary	10.00 m	10.50 m	Inside the indicative setback envelope	Codes SEPP Inland Code primary road. Indicative. Check with council.
Side boundary 1	2.50 m	428.04 m	Inside the indicative setback envelope	Codes SEPP Inland Code side. Indicative. Check with council.
Side boundary 2	2.50 m	802.11 m	Inside the indicative setback envelope	Codes SEPP Inland Code side. Indicative. Check with council.
Side boundary 3	2.50 m	857.50 m	Inside the indicative setback envelope	Codes SEPP Inland Code side. Indicative. Check with council.
Side boundary 4	2.50 m	860.99 m	Inside the indicative setback envelope	Codes SEPP Inland Code side. Indicative. Check with council.
Rear boundary	15.00 m	437.00 m	Inside the indicative setback envelope	Codes SEPP Inland Code rear. Indicative. Check with council.
Side boundary 5	2.50 m	314.51 m	Inside the indicative setback envelope	Codes SEPP Inland Code side. Indicative. Check with council.
Side boundary 6	2.50 m	161.26 m	Inside the indicative setback envelope	Codes SEPP Inland Code side. Indicative. Check with council.

Rule set: Gunnedah Shire Council, Codes SEPP Inland Code (complying development pathway; exclusions such as bushfire, flood and heritage apply). State Environmental Planning Policy (Exempt and Complying Development Codes) 2008, Part 3D Inland Code (as retrieved 11/11/2026; Indicative. Check with council.). Provided distances are the least distance from the building to each boundary, measured from the walls and rooms. A result here is not an approval.

ITEMS TO CONFIRM

ITEM	WHO CONFIRMS
Front: not yet confirmed with council	Council
Side: Table minimum shown. Parts of a building more than 4.5 m above ground need a larger side setback formula not captured)	Council
Rear: not yet confirmed with council	Council
Garage: not yet confirmed with council	Council
Bushfire attack level, flood, heritage and other overlays	Council or certifier
Easements, sewer and stormwater connection points, Before You Dig Australia plans	Surveyor and authorities
Registered survey: boundaries, levels, trees and existing structures	Registered surveyor
Crossover location, width and levels; driveway grade	Council
Structure, bracing and footings	Structural engineer

Sample Builder Homes

Prepared with Glide Inside

PROJECT
SINGLE STOREY, 4 BEDROOM
756 QUIA ROAD GUNNEDAH NSW
LOT 3 DP 263990

CLIENT
A Sample Client

DRAWING TITLE
SITE ANALYSIS AND SETBACKS

REV	DATE	DESCRIPTION	DRN	CHK	APP
A	11/11/2026	Concept			

NOT CHECKED. NOT APPROVED.

DRAWING NUMBER: **GI-L3DP263990-A-007**
REV: **A**
STATUS: **CONCEPT**
DATE: **11/11/2026**
DRAWN:
CHECKED:
APPROVED:
JOB NO.:
SCALE: **1:10000 @ A3**
SHEET: **7 OF 8**
SIZE: **A3**

CONCEPT ONLY. TO BE VERIFIED BY A SUITABLY QUALIFIED PERSON BEFORE ANY USE FOR APPROVAL OR CONSTRUCTION. Not a survey. Not a development application drawing.
Cadastre, imagery and contours: NSW Spatial Services (CC BY). Aerial underlay: NSW Spatial Services (c) Department of Customer Service 2020. Sample picture only. Reduced resolution, not for measurement.

AREAS AND SITE COVERAGE

ITEM	AREA
Ground floor area	237.8 m²
Total internal floor area	**237.8 m²**
Outdoor areas	36.0 m²
Garage (included above)	37.2 m²
Building footprint (ground level)	273.8 m²
Site area	50.93 ha
Site coverage (footprint over site area)	**0.1 %**
Roof area (from the model, sloped)	684.0 m²
Driveway within the lot (indicative)	51.0 m²
Crossover in the road reserve (indicative)	37.1 m²
Remaining site area (soft and other hard)	50.90 ha

Areas are measured from the room polygons in the design. Site coverage uses the cadastre area unless a registered area is stated. Council definitions of floor area and coverage can differ: check with council.

SITE AREA BREAKDOWN



- Building footprint: 274 m² (0 %)
- Driveway within the lot: 51 m² (0 %)
- Remaining site area: 50.90 ha (100 %)

ROOM SCHEDULE

LEVEL	ROOM	TYPE	M²
Ground	Master	Bedroom	24.96
Ground	Ensuite	Ensuite	6.72
Ground	Walk-in robe	Robe	5.76
Ground	Kitchen, dining and family	Family	50.96
Ground	Hall	Hall	24.84
Ground	Bed 4	Bedroom	13.60
Ground	Laundry	Laundry	8.84
Ground	Bathroom	Bathroom	8.40
Ground	WC	WC	3.36
Ground	Mud room	Store	3.36
Ground	Entry	Entry	5.76
Ground	Lounge	Living	21.60
Ground	Bed 2	Bedroom	11.22
Ground	Bed 3	Bedroom	11.22
Ground	Garage	Garage	37.20
Ground	Alfresco	Alfresco	36.00

16 rooms. Areas in square metres to two places.

DOOR AND WINDOW SCHEDULE

TYPE	W x H (MM)	SILL	QTY
Door	820 x 2040		7
Cavity door	820 x 2040		5
Door	870 x 2040		1
Garage door	4800 x 2100		1
Opening	1500 x 2040		1
Opening	1800 x 2040		1
Sliding door	3000 x 2100		1
Awning window	600 x 600	1500	1
Awning window	1200 x 600	1500	2
Sliding window	1800 x 1200	900	6
Sliding window	1800 x 900	1200	1
Sliding window	2400 x 1200	900	1

Total openings: 28

Colour scheme: Standard colours

Roof and trim in charcoal. Walls as drawn in the design.

SCHEDULE NOTES

- Sizes are the nominal opening width and height in millimetres. The sill is the height of the sill above the finished floor level.
- Glazing, frame and hardware are to be selected by the builder. Window and door energy ratings, bushfire and wind rating requirements are not assessed here.
- Room names and types are those in the design. Areas are internal, measured to the face of the wall.

Sample Builder Homes

Prepared with Glide Inside

PROJECT
SINGLE STOREY, 4 BEDROOM
756 QUIA ROAD GUNNEDAH NSW
LOT 3 DP 263990

CLIENT
A Sample Client

DRAWING TITLE
SCHEDULES

REV	DATE	DESCRIPTION	DRN	CHK	APP
A	11/11/2026	Concept			

NOT CHECKED. NOT APPROVED.

DRAWING NUMBER **GI-L3DP263990-A-008** | REV **A** | STATUS **CONCEPT**

DATE **11/11/2026** | DRAWN | CHECKED | APPROVED | JOB NO.

SCALE **NTS** | SHEET **8 OF 8** | SIZE **A3**

CONCEPT ONLY. TO BE VERIFIED BY A SUITABLY QUALIFIED PERSON BEFORE ANY USE FOR APPROVAL OR CONSTRUCTION. Not a survey. Not a development application drawing.
Cadastre, imagery and contours: NSW Spatial Services (CC BY). Aerial underlay: NSW Spatial Services (c) Department of Customer Service 2020. Sample picture only. Reduced resolution, not for measurement.