CONCEPT PLAN SET

SAMPLE RESIDENCE


14 Sample Street Calala NSW
LOT 24 DP 1234567

Client: A Sample Client
Council: TAMWORTH REGIONAL
Zone: R1 General Residential
Site area: 800 m2
Issue: Concept, revision A, 11.11.26

DRAWING LIST

DRAWING NUMBER	TITLE	SCALE
GI-TAM24-A-001	COVER SHEET AND DRAWING LIST	NTS
GI-TAM24-A-002	SITE PLAN	AS SHOWN
GI-TAM24-A-003	GROUND FLOOR PLAN	1:100 @ A3
GI-TAM24-A-004	FIRST FLOOR PLAN	1:100 @ A3
GI-TAM24-A-005	ROOF PLAN	AS SHOWN
GI-TAM24-A-006	ELEVATIONS	AS SHOWN
GI-TAM24-A-007	SECTION	AS SHOWN
GI-TAM24-A-008	SITE ANALYSIS AND SETBACKS	NTS
GI-TAM24-A-009	SCHEDULES	NTS

LOCALITY

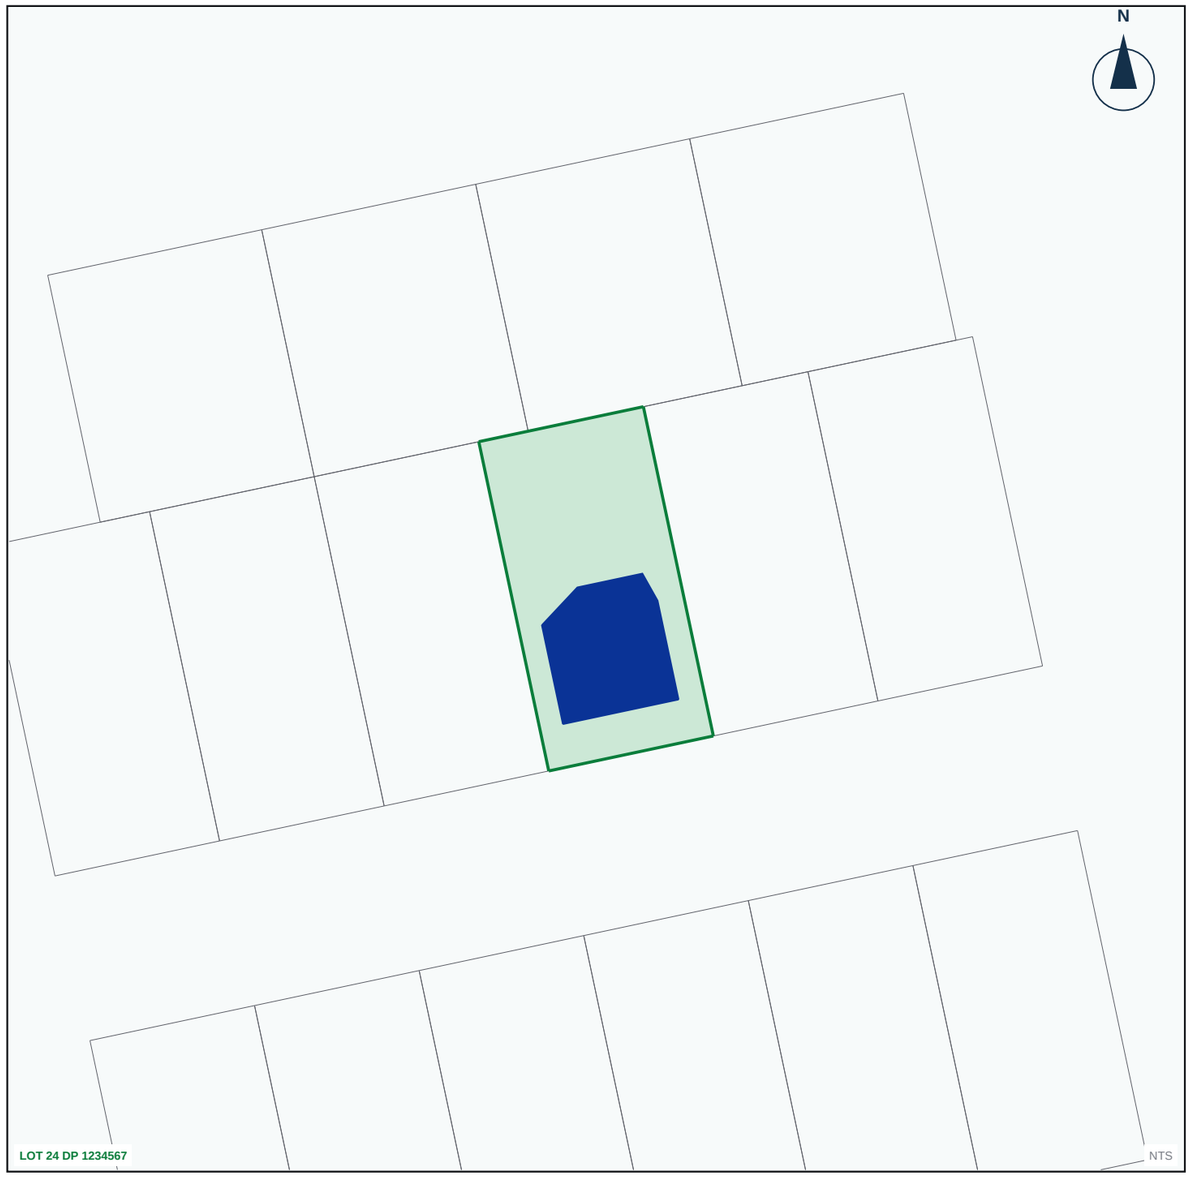

This is a concept design for discussion. Setbacks, levels and boundaries are indicative and have not been checked by a surveyor, certifier or council. Where a council rule is marked check with council it has not been confirmed.

Prepared with Glide Inside

Sample Builder Homes

Prepared with Glide Inside
Glide Inside

PROJECT
SAMPLE RESIDENCE
14 SAMPLE STREET CALALA NSW
LOT 24 DP 1234567

CLIENT
A Sample Client

DRAWING TITLE
COVER SHEET AND DRAWING LIST


REV	DATE	DESCRIPTION	DRN	CHK	APP
A	11.11.26	Concept	AB	CD	

DRAWING NUMBER: **GI-TAM24-A-001**
REV: **A**
STATUS: **CONCEPT**
DATE: **11.11.26**
DRAWN: **AB**
CHECKED: **CD**
APPROVED:
JOB NO.: **TAM24**
SCALE: **NTS**
SHEET: **1 OF 9**
SIZE: **A3**

CONCEPT ONLY. TO BE VERIFIED BY A SUITABLY QUALIFIED PERSON BEFORE ANY USE FOR APPROVAL OR CONSTRUCTION. Not a survey. Not a development application drawing.

Cadastre, imagery and contours: NSW Spatial Services (CC BY).

SITE PLAN 1:300 @ A3

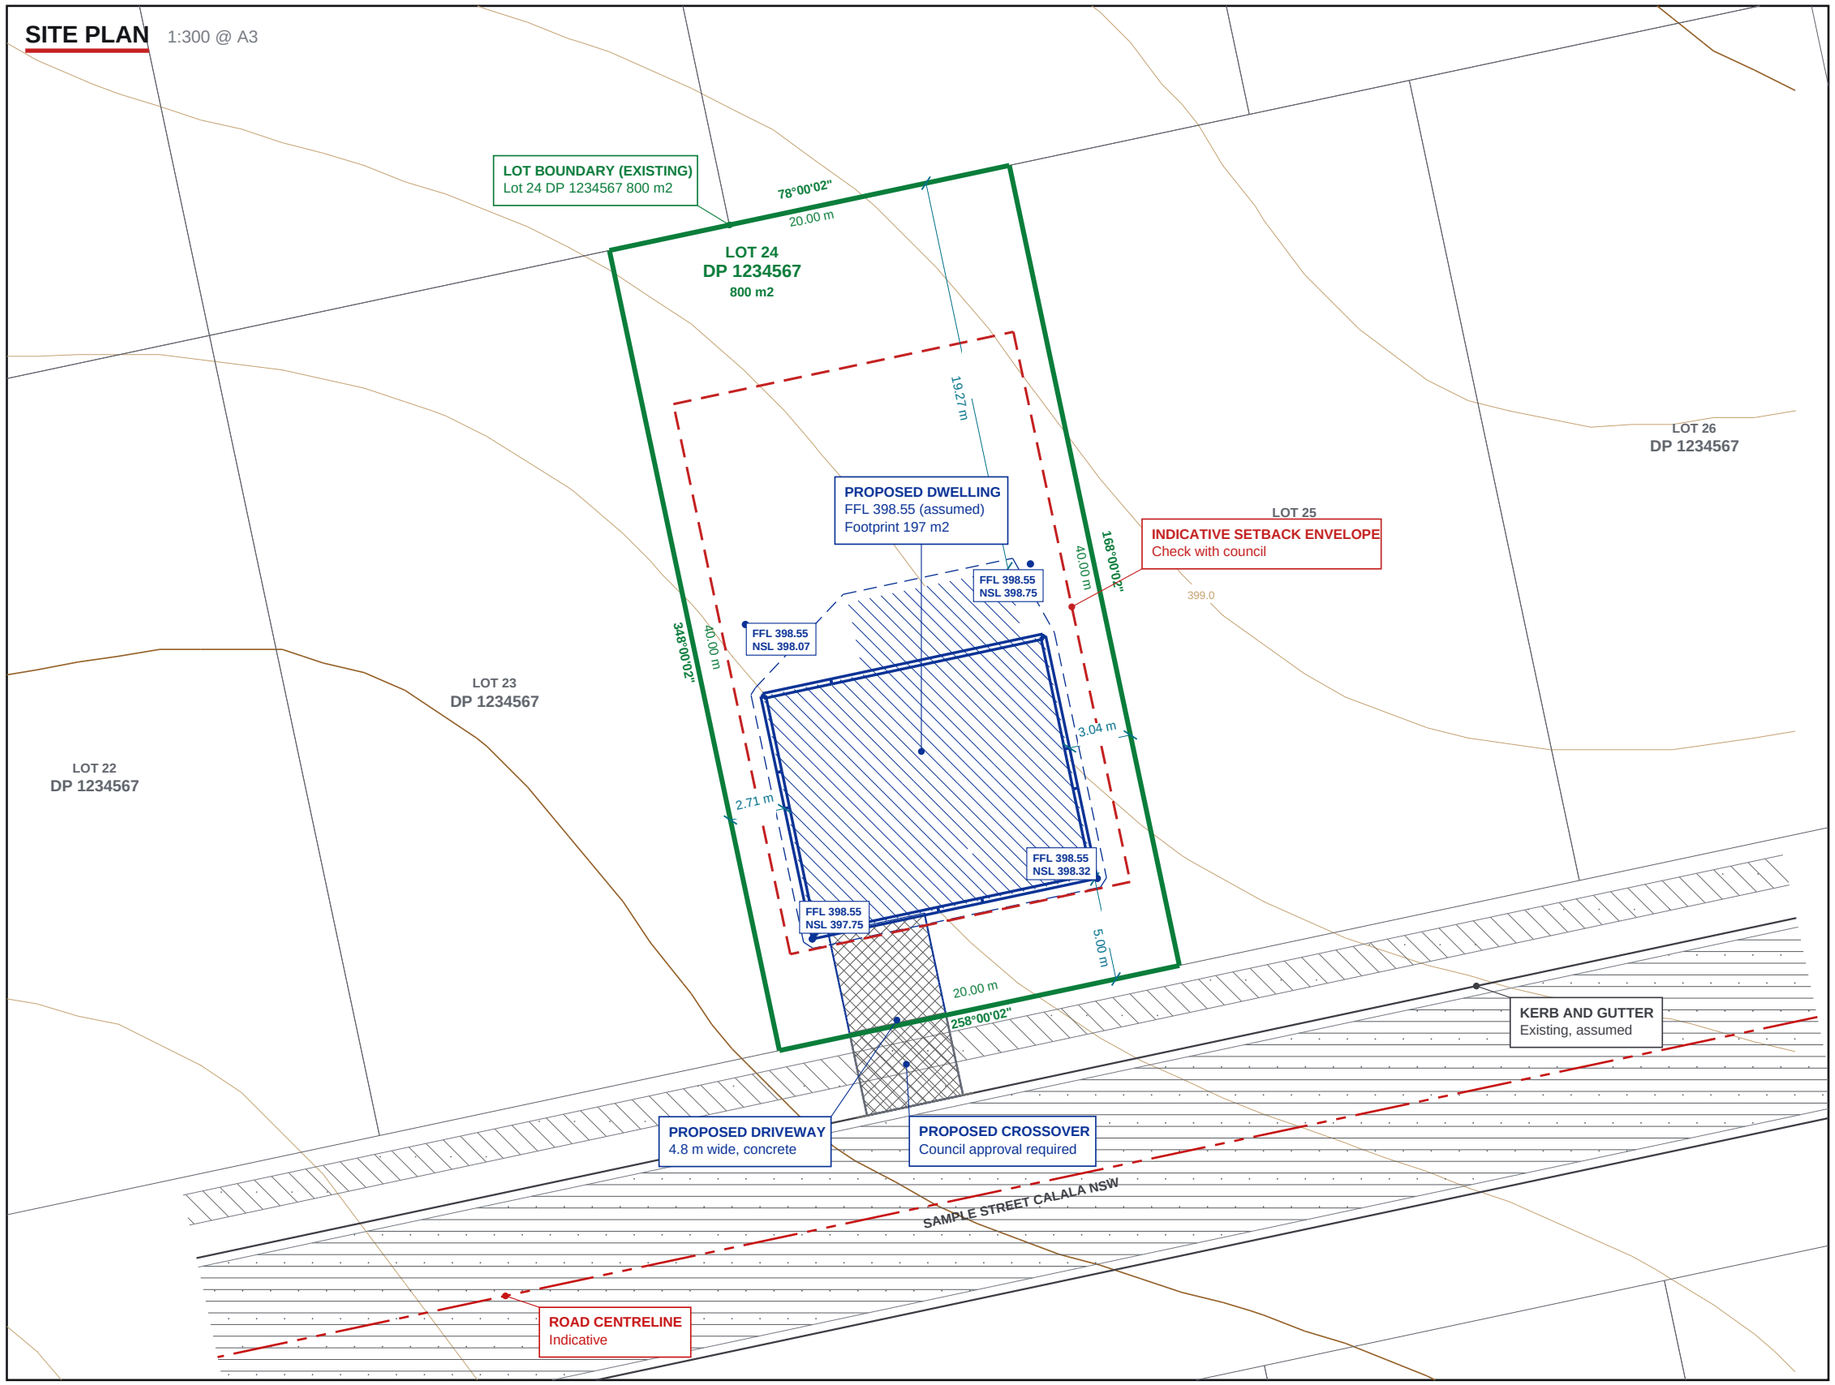

N


SCALE 1:300 @ A3

North is MGA grid north.

Plan up is north.

0 5 10 15 20 m

KEY PLAN

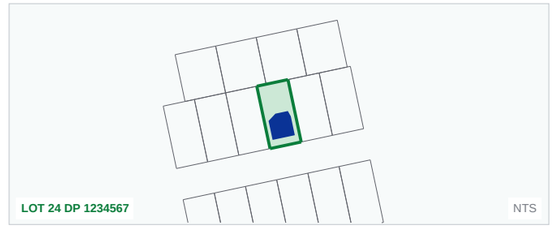

LEGEND

- Lot boundary (existing)
- Neighbouring lot boundary
- Indicative setback envelope
- Road centreline (indicative)
- Kerb and gutter
- Contour (minor, major)
- Dimension to boundary
- Proposed works
- Hardstand (driveway)
- Concrete (crossover, footpath)
- Bitumen (road)

NOTES

1. Concept only. To be verified by a suitably qualified person before any use for approval or construction.
2. Boundaries are from the cadastre, are indicative only, and are not a survey. A registered survey is required.
3. Setbacks: Tamworth Regional Council Codes SEPP Inland Code (complying development pathway; exclusions such as bushfire, flood and heritage apply). The red envelope is indicative. Where a rule is marked "check with council" the figure has not been confirmed with the council.
4. Front 4.5 m: Codes SEPP Inland Code cl 3D.21(1)-(3) primary road (check with council).
5. Side 1.5 m: Codes SEPP Inland Code cl 3D.21(7)-(8) side (check with council).
6. Rear 8 m: Codes SEPP Inland Code cl 3D.21(14) rear (check with council).
7. Contours: NSW 5 m DEM, indicative only; detailed survey required. Vertical accuracy: not stated by the service. Datum: AHD (orthometric, per service heightModelInfo).
8. FFL 398.55 m AHD is assumed from the ground level at the house, not designed. NSL is the natural surface level from the terrain model at each house corner.
9. Services, easements, trees, flood and bushfire overlays are not shown. Dial Before You Dig plans and a section 10.7 or equivalent certificate are required.
10. Driveway and crossover are indicative. Crossover location, width and levels need council approval.

Sample Builder Homes

Prepared with Glide Inside

PROJECT
SAMPLE RESIDENCE
14 SAMPLE STREET CALALA NSW
LOT 24 DP 1234567

CLIENT
A Sample Client


DRAWING TITLE
SITE PLAN

REV	DATE	DESCRIPTION	DRN	CHK	APP
A	11.11.26	Concept	AB	CD	

DRAWING NUMBER **GI-TAM24-A-002**
REV **A**
STATUS **CONCEPT**
DATE **11.11.26**
DRAWN **AB**
CHECKED **CD**
APPROVED
JOB NO. **TAM24**
SCALE **AS SHOWN**
SHEET **2 OF 9**
SIZE **A3**

CONCEPT ONLY. TO BE VERIFIED BY A SUITABLY QUALIFIED PERSON BEFORE ANY USE FOR APPROVAL OR CONSTRUCTION. Not a survey. Not a development application drawing.

Cadastre, imagery and contours: NSW Spatial Services (CC BY).

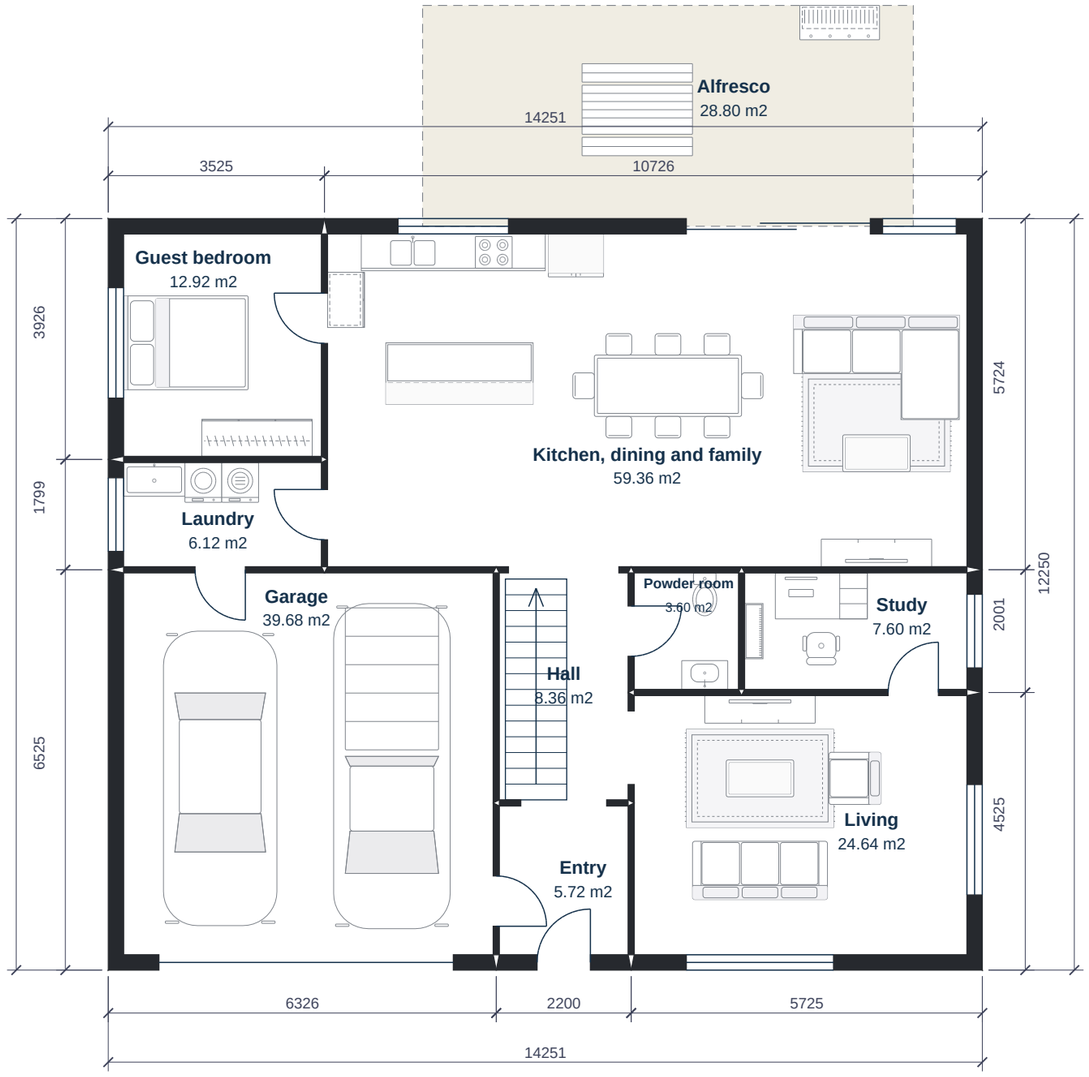

GROUND FLOOR PLAN

1:100 @ A3


0 1 2 3 4 5 m

N

Sample Builder Homes	PROJECT **SAMPLE RESIDENCE** 14 SAMPLE STREET CALALA NSW LOT 24 DP 1234567	REV	DATE	DESCRIPTION	DRN	CHK	APP	DRAWING NUMBER **GI-TAM24-A-003**	REV **A**	STATUS **CONCEPT**
	CLIENT **A Sample Client**							DATE **11.11.26**	DRAWN **AB**	CHECKED **CD**
	DRAWING TITLE **GROUND FLOOR PLAN**							APPROVED	JOB NO. **TAM24**	
Prepared with Glide Inside Glide Inside		A	11.11.26	Concept	AB	CD		SCALE **1:100 @ A3**	SHEET **3 OF 9**	SIZE **A3**

CONCEPT ONLY. TO BE VERIFIED BY A SUITABLY QUALIFIED PERSON BEFORE ANY USE FOR APPROVAL OR CONSTRUCTION. Not a survey. Not a development application drawing.

Cadastre, imagery and contours: NSW Spatial Services (CC BY).

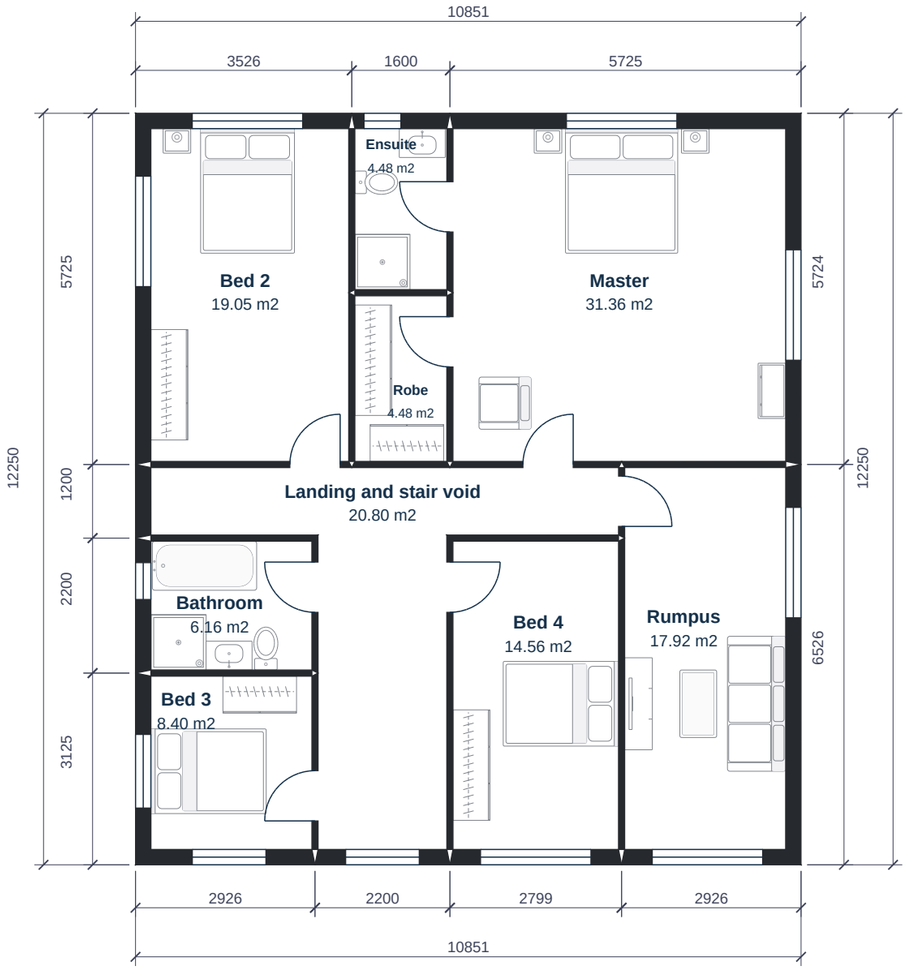

FIRST FLOOR PLAN

1:100 @ A3

0 1 2 3 4 5 m

N


Sample Builder Homes	PROJECT **SAMPLE RESIDENCE** 14 SAMPLE STREET CALALA NSW LOT 24 DP 1234567	REV	DATE	DESCRIPTION	DRN	CHK	APP	DRAWING NUMBER **GI-TAM24-A-004**	REV **A**	STATUS **CONCEPT**
Prepared with Glide Inside Glide Inside	CLIENT **A Sample Client**	A	11.11.26	Concept	AB	CD		DATE **11.11.26**	DRAWN **AB**	CHECKED **CD**	APPROVED	JOB NO. **TAM24**
	DRAWING TITLE **FIRST FLOOR PLAN**							SCALE **1:100 @ A3**	SHEET **4 OF 9**	SIZE **A3**

CONCEPT ONLY. TO BE VERIFIED BY A SUITABLY QUALIFIED PERSON BEFORE ANY USE FOR APPROVAL OR CONSTRUCTION. Not a survey. Not a development application drawing.

Cadastre, imagery and contours: NSW Spatial Services (CC BY).

ROOF PLAN 1:150 @ A3

hip roof, 22.5 degree pitch, 450 mm eaves overhang. Roof area from the model 335 m2. Arrows show the fall.

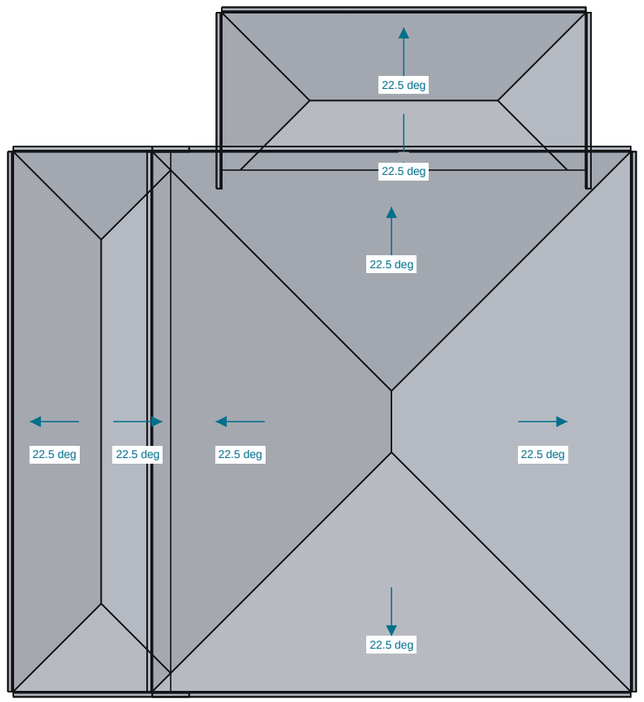

0 2 4 6 8 10 m

Sample Builder Homes

Prepared with Glide Inside

Glide Inside

PROJECT
SAMPLE RESIDENCE
14 SAMPLE STREET CALALA NSW
LOT 24 DP 1234567

CLIENT
A Sample Client

DRAWING TITLE
ROOF PLAN

REV	DATE	DESCRIPTION	DRN	CHK	APP
A	11.11.26	Concept	AB	CD	

DRAWING NUMBER **GI-TAM24-A-005**
REV **A**
STATUS **CONCEPT**
DATE **11.11.26**
DRAWN **AB**
CHECKED **CD**
APPROVED
JOB NO. **TAM24**
SCALE **AS SHOWN**
SHEET **5 OF 9**
SIZE **A3**

CONCEPT ONLY. TO BE VERIFIED BY A SUITABLY QUALIFIED PERSON BEFORE ANY USE FOR APPROVAL OR CONSTRUCTION. Not a survey. Not a development application drawing.


Cadastre, imagery and contours: NSW Spatial Services (CC BY).




NORTH ELEVATION 1:150 @ A3



EAST ELEVATION 1:150 @ A3

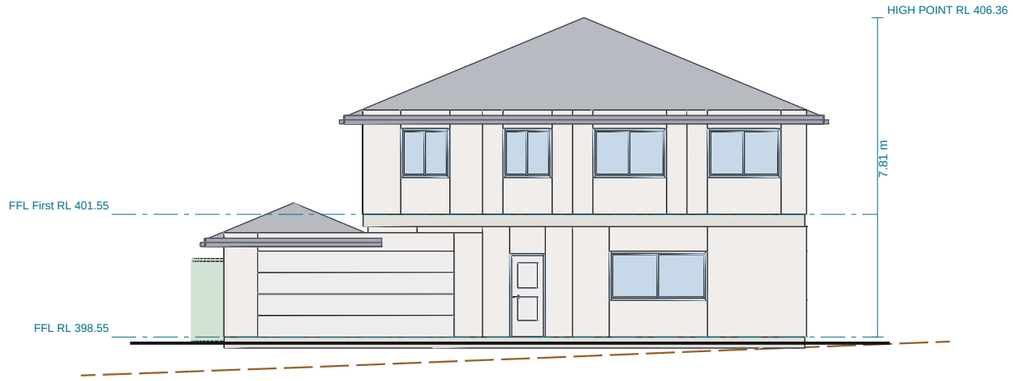

SOUTH ELEVATION 1:150 @ A3

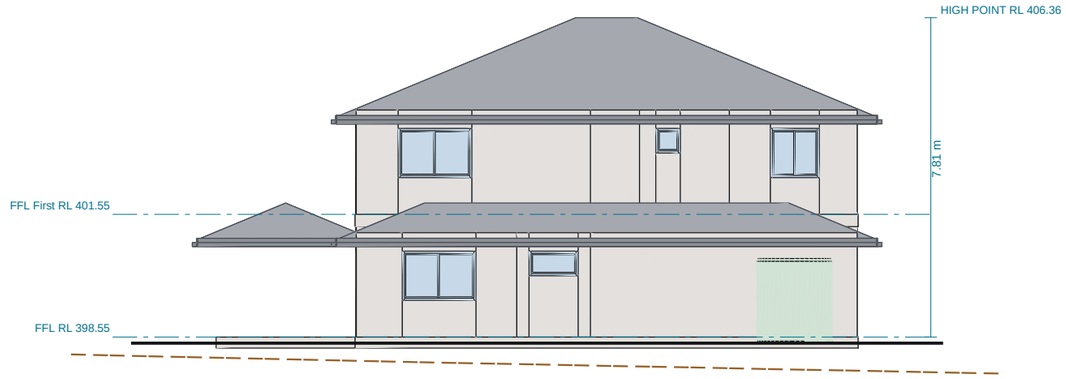

WEST ELEVATION 1:150 @ A3

Sample Builder Homes

Prepared with Glide Inside

PROJECT
SAMPLE RESIDENCE
14 SAMPLE STREET CALALA NSW
LOT 24 DP 1234567

CLIENT
A Sample Client

DRAWING TITLE
ELEVATIONS


REV	DATE	DESCRIPTION	DRN	CHK	APP
A	11.11.26	Concept	AB	CD	

DRAWING NUMBER **GI-TAM24-A-006**
REV **A**
STATUS **CONCEPT**
DATE **11.11.26**
DRAWN **AB**
CHECKED **CD**
APPROVED
JOB NO. **TAM24**
SCALE **AS SHOWN**
SHEET **6 OF 9**
SIZE **A3**

CONCEPT ONLY. TO BE VERIFIED BY A SUITABLY QUALIFIED PERSON BEFORE ANY USE FOR APPROVAL OR CONSTRUCTION. Not a survey. Not a development application drawing.
Cadastre, imagery and contours: NSW Spatial Services (CC BY).

SECTION A-A 1:100 @ A3

Cut across the centre of the house, looking south. Heavy lines are cut elements.

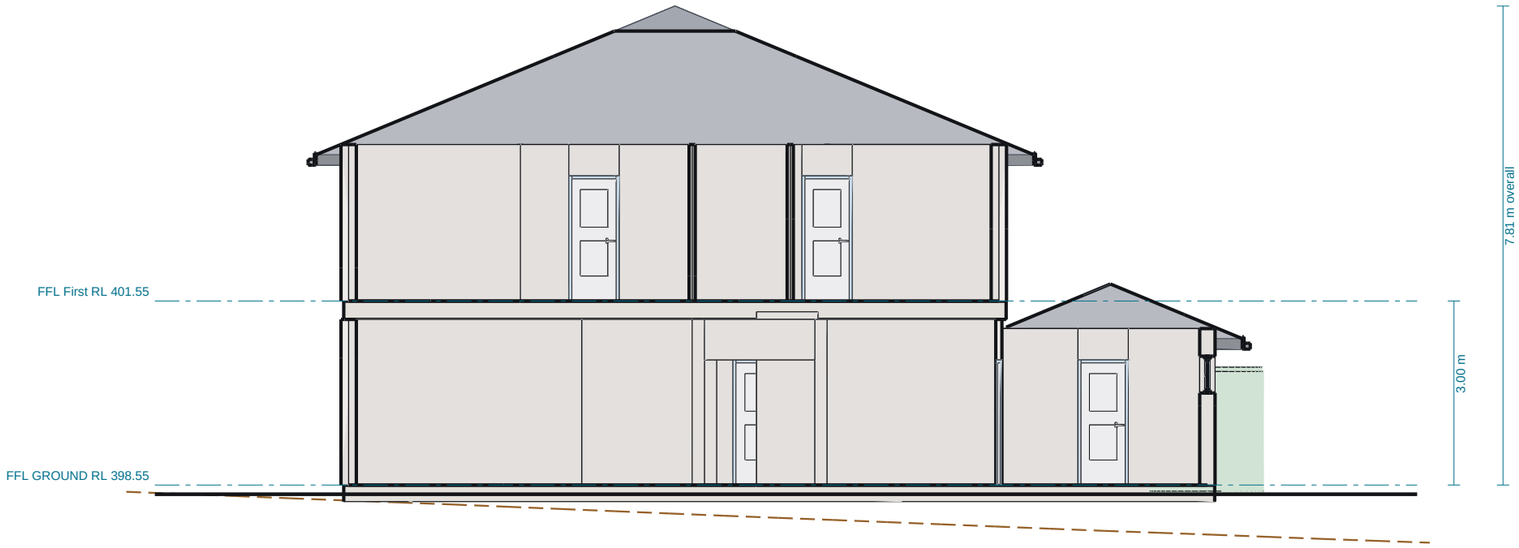

0 1 2 3 4 5 m

Sample Builder Homes

Prepared with Glide Inside

Glide Inside

PROJECT
SAMPLE RESIDENCE
14 SAMPLE STREET CALALA NSW
LOT 24 DP 1234567

CLIENT
A Sample Client

DRAWING TITLE
SECTION


REV	DATE	DESCRIPTION	DRN	CHK	APP
A	11.11.26	Concept	AB	CD	

DRAWING NUMBER: **GI-TAM24-A-007**
REV: **A**
STATUS: **CONCEPT**
DATE: **11.11.26**
DRAWN: **AB**
CHECKED: **CD**
APPROVED:
JOB NO.: **TAM24**
SCALE: **AS SHOWN**
SHEET: **7 OF 9**
SIZE: **A3**

CONCEPT ONLY. TO BE VERIFIED BY A SUITABLY QUALIFIED PERSON BEFORE ANY USE FOR APPROVAL OR CONSTRUCTION. Not a survey. Not a development application drawing.

Cadastre, imagery and contours: NSW Spatial Services (CC BY).

SITE ANALYSIS NTS

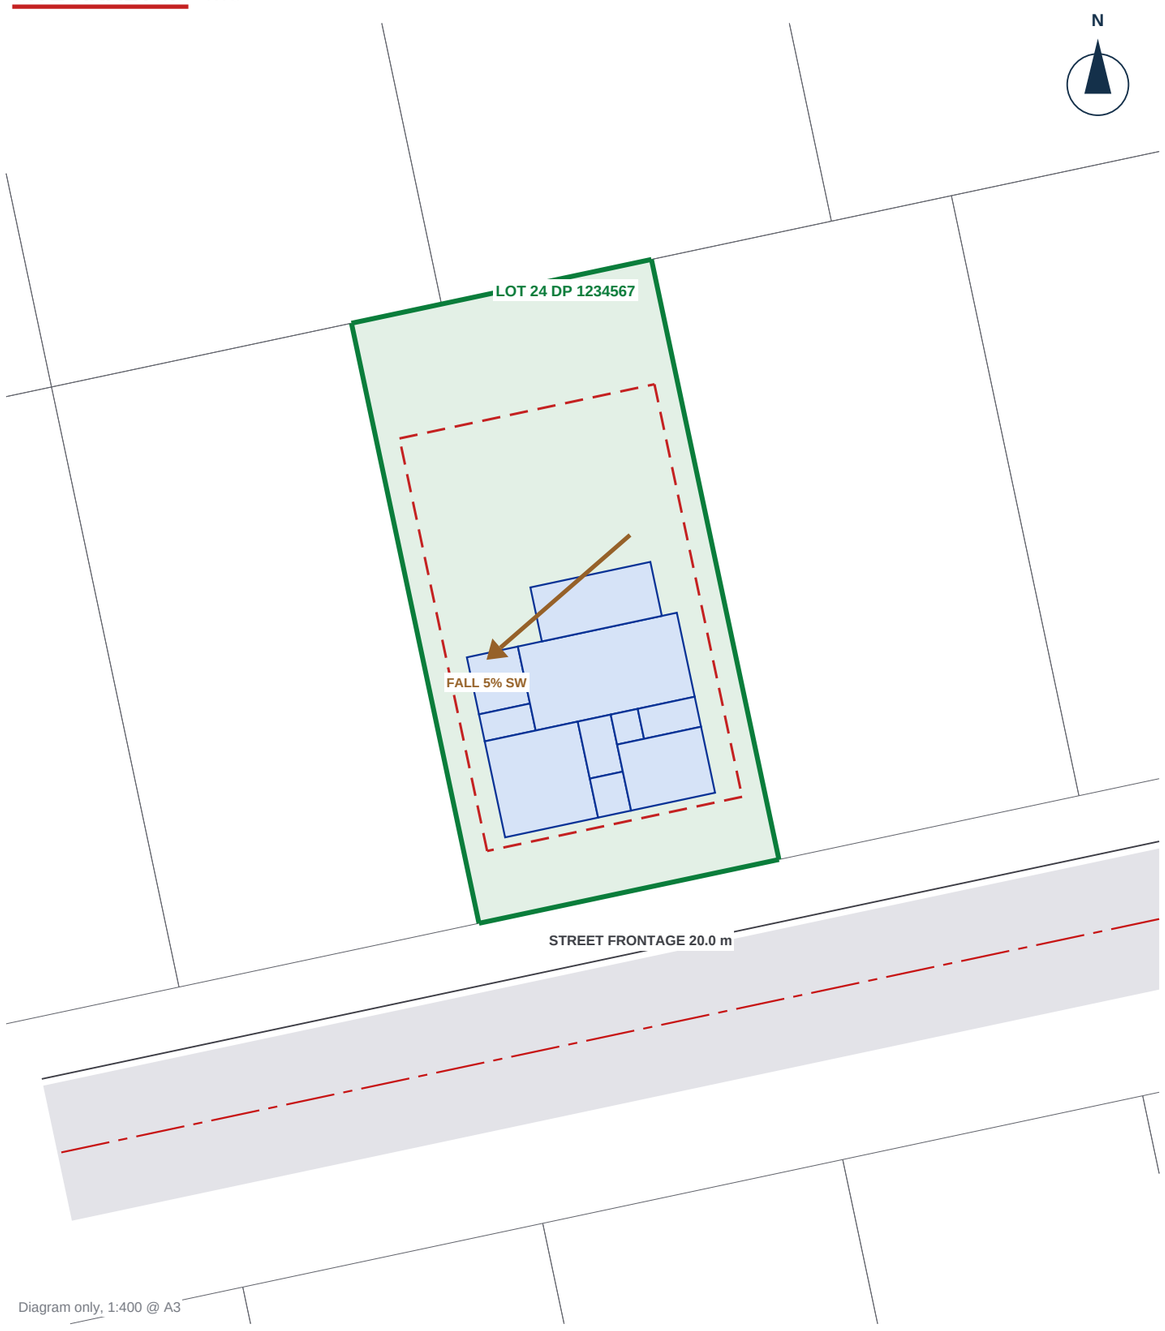

SITE FACTS

ITEM	DETAIL
Address	14 Sample Street Calala NSW
Lot and DP	LOT 24 DP 1234567
Council	TAMWORTH REGIONAL
Zone	R1 General Residential
Site area	800 m2 (registered 800 m2)
Frontage and depth	20.0 m by 40.0 m
Corner lot	No
Ground fall	1.83 m across the lot, 5% towards the sw
Floor level	FFL 398.55 m AHD (assumed)
Overlays	Bushfire, flood, heritage and easements not checked

SETBACKS: REQUIRED AND PROVIDED

BOUNDARY	REQUIRED	PROVIDED	RESULT	SOURCE AND CHECK
Rear boundary	8.00 m	19.27 m	Inside the indicative setback envelope	Codes SEPP Inland Code cl 3D.21(14) rear. Check with council.
Side boundary 1	1.50 m	3.04 m	Inside the indicative setback envelope	Codes SEPP Inland Code cl 3D.21(7)-(8) side. Check with council.
Front boundary	4.50 m	5.00 m	Inside the indicative setback envelope	Codes SEPP Inland Code cl 3D.21(1)-(3) primary road. Check with council.
Side boundary 2	1.50 m	2.71 m	Inside the indicative setback envelope	Codes SEPP Inland Code cl 3D.21(7)-(8) side. Check with council.

Rule set: Tamworth Regional Council, Codes SEPP Inland Code (complying development pathway; exclusions such as bushfire, flood and heritage apply). State Environmental Planning Policy (Exempt and Complying Development Codes) 2008, Part 3D Inland Code (as retrieved 11/11/2026; currency against the in-force text not verified). Provided distances are the least distance from the building to each boundary, measured from the walls and rooms. A pass here is not an approval.

ITEMS TO CONFIRM

ITEM	WHO CONFIRMS
front: not yet confirmed with council	Council
side: Table minimum shown. Parts of a building more than 4.5 m above ground need a larger side setback (cl 3D.21(8) formula not captured)	Council
rear: not yet confirmed with council	Council
garage: not yet confirmed with council	Council
Bushfire attack level, flood, heritage and other overlays	Council or certifier
Easements, sewer and stormwater connection points, Dial Before You Dig plans	Surveyor and authorities
Registered survey: boundaries, levels, trees and existing structures	Registered surveyor
Crossover location, width and levels; driveway grade	Council
Structure, bracing and footings	Structural engineer

Sample Builder Homes

Prepared with Glide Inside

PROJECT
SAMPLE RESIDENCE
14 SAMPLE STREET CALALA NSW
LOT 24 DP 1234567

CLIENT
A Sample Client

DRAWING TITLE
SITE ANALYSIS AND SETBACKS

REV	DATE	DESCRIPTION	DRN	CHK	APP
A	11.11.26	Concept	AB	CD	

DRAWING NUMBER **GI-TAM24-A-008** | REV **A** | STATUS **CONCEPT**

DATE	DRAWN	CHECKED	APPROVED	JOB NO.
11.11.26	AB	CD		TAM24

SCALE	SHEET	SIZE
NTS	8 OF 9	A3

CONCEPT ONLY. TO BE VERIFIED BY A SUITABLY QUALIFIED PERSON BEFORE ANY USE FOR APPROVAL OR CONSTRUCTION. Not a survey. Not a development application drawing.

Cadastre, imagery and contours: NSW Spatial Services (CC BY).

AREAS AND SITE COVERAGE

ITEM	AREA
Ground floor area	168.0 m2
First floor area	127.2 m2
Total internal floor area	**295.2 m2**
Outdoor areas	28.8 m2
Garage (included above)	39.7 m2
Building footprint (ground level)	196.8 m2
Site area	800 m2
Site coverage (footprint over site area)	**24.6 %**
Roof area (from the model, sloped)	335.3 m2
Driveway (indicative)	43.8 m2
Remaining site area (soft and other hard)	559 m2

Areas are measured from the room polygons in the design. Site coverage uses the cadastre area unless a registered area is stated. Council definitions of floor area and coverage can differ: check with council.

ROOM SCHEDULE

LEVEL	ROOM	TYPE	M2
Ground	Guest bedroom	Bedroom	12.92
Ground	Laundry	Laundry	6.12
Ground	Kitchen, dining and family	Family	59.35
Ground	Garage	Garage	39.68
Ground	Hall	Hall	8.36
Ground	Entry	Entry	5.72
Ground	Powder room	WC	3.60
Ground	Study	Study	7.60
Ground	Living	Living	24.64
Ground	Alfresco	Alfresco	28.80
First	Bed 2	Bedroom	19.04
First	Ensuite	Ensuite	4.48
First	Robe	Robe	4.48
First	Master	Bedroom	31.36
First	Bathroom	Bathroom	6.16
First	Bed 3	Bedroom	8.40
First	Bed 4	Bedroom	14.56
First	Rumpus	Rumpus	17.92
First	Landing and stair void	Hall	20.80

DOOR AND WINDOW SCHEDULE

TYPE	W x H MM	SILL	QTY
Door	820 x 2040	-	12
Door cavity	820 x 2040	-	2
Door	870 x 2040	-	1
Garage door	4800 x 2100	-	1
Opening	1200 x 2040	-	1
Opening	1400 x 2040	-	1
Opening	1800 x 2040	-	1
Sliding door sliding	3000 x 2100	-	1
Window awning	600 x 600	1500	2
Window sliding	1200 x 1200	900	5
Window awning	1200 x 600	1500	1
Window sliding	1800 x 900	1200	1
Window sliding	1800 x 1200	900	9
Window sliding	2400 x 1200	900	1

Sample Builder Homes

Prepared with Glide Inside

PROJECT
SAMPLE RESIDENCE
14 SAMPLE STREET CALALA NSW
LOT 24 DP 1234567

CLIENT
A Sample Client

DRAWING TITLE
SCHEDULES

REV	DATE	DESCRIPTION	DRN	CHK	APP
A	11.11.26	Concept	AB	CD	

DRAWING NUMBER **GI-TAM24-A-009** | REV **A** | STATUS **CONCEPT**

DATE **11.11.26** | DRAWN **AB** | CHECKED **CD** | APPROVED | JOB NO. **TAM24**

SCALE **NTS** | SHEET **9 OF 9** | SIZE **A3**

CONCEPT ONLY. TO BE VERIFIED BY A SUITABLY QUALIFIED PERSON BEFORE ANY USE FOR APPROVAL OR CONSTRUCTION. Not a survey. Not a development application drawing.

Cadastre, imagery and contours: NSW Spatial Services (CC BY).