CONCEPT PLAN SET

SAMPLE RESIDENCE


14 Sample Street Calala NSW
Lot 27 DP 1234567

Client: A Sample Client
Council: Tamworth Regional
Zone: R5 Large Lot Residential
Site area: 2000 m^2
Issue: Concept, revision A, 11/11/2026

DRAWING LIST

DRAWING NUMBER	TITLE	SCALE
GI-TAM24-A-001	Cover sheet and drawing list	AS SHOWN
GI-TAM24-A-002	Site plan	1:500 @ A3
GI-TAM24-A-003	Ground floor plan	1:100 @ A3
GI-TAM24-A-004	First floor plan	1:100 @ A3
GI-TAM24-A-005	Roof plan	1:100 @ A3
GI-TAM24-A-006	Elevations	1:150 @ A3
GI-TAM24-A-007	Section	1:50 @ A3
GI-TAM24-A-008	Site analysis and setbacks	1:500 @ A3
GI-TAM24-A-009	Schedules	NTS

LOCALITY

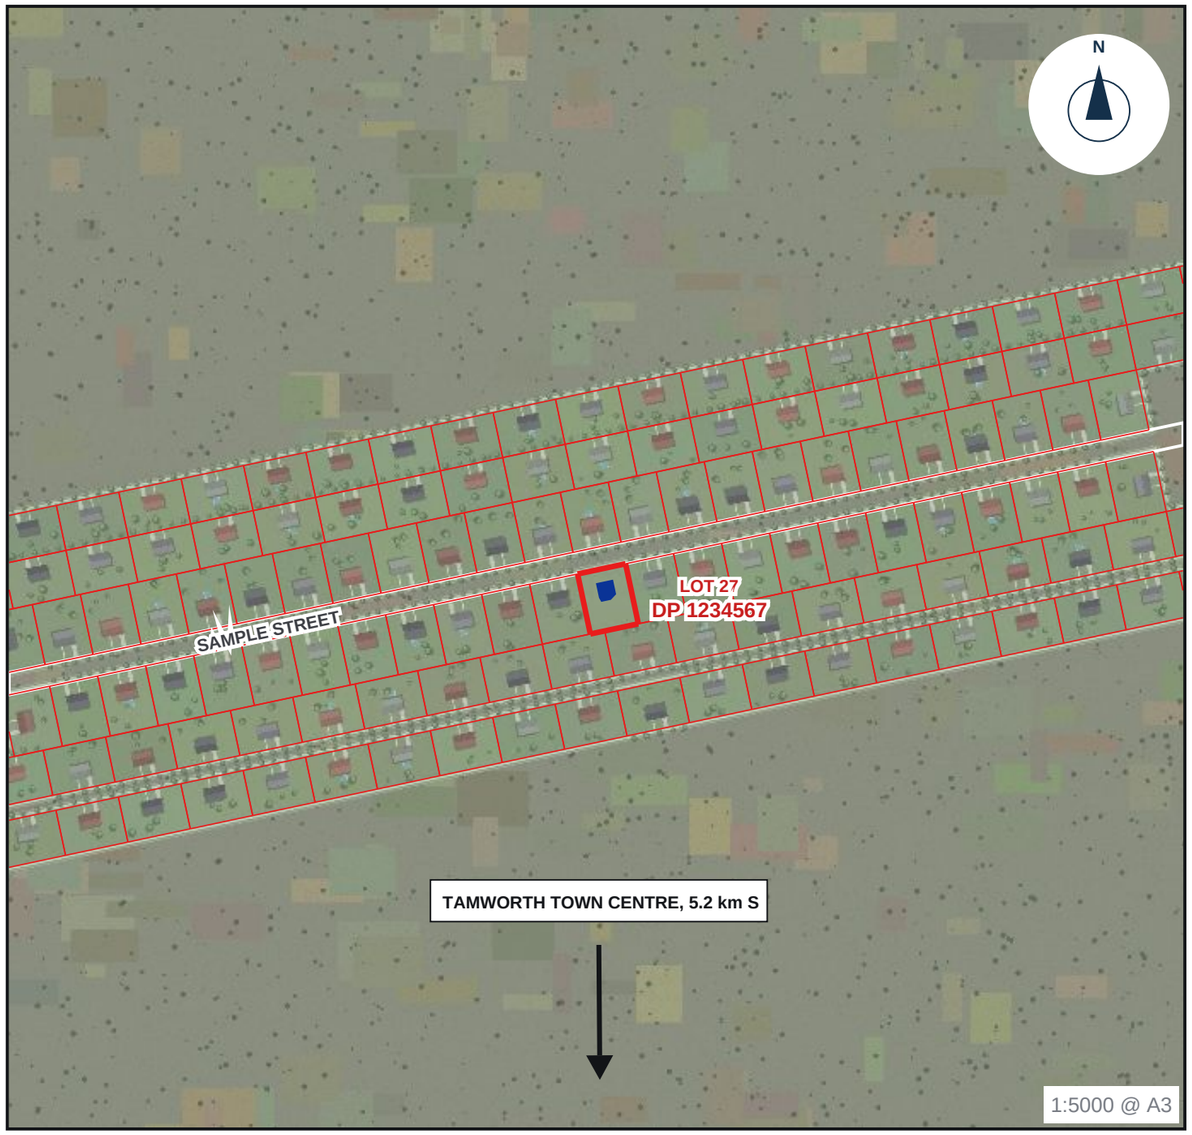

This is a concept design for discussion. Setbacks, levels and boundaries are indicative and have not been checked by a surveyor, certifier or council. Where a council rule is marked check with council it has not been confirmed.

Prepared with Glide Inside

Glide Inside

Prepared with Glide Inside

PROJECT
SAMPLE RESIDENCE
14 SAMPLE STREET CALALA NSW
LOT 27 DP 1234567

CLIENT
A Sample Client

DRAWING TITLE
COVER SHEET AND DRAWING LIST


REV	DATE	DESCRIPTION	DRN	CHK	APP
A	11/11/2026	Concept			

NOT CHECKED. NOT APPROVED.

DRAWING NUMBER: **GI-TAM24-A-001**
REV: **A**
STATUS: **CONCEPT**
DATE: **11/11/2026**
DRAWN:
CHECKED:
APPROVED:
JOB NO.: **TAM24**
SCALE: **AS SHOWN**
SHEET: **1 OF 9**
SIZE: **A3**

CONCEPT ONLY. TO BE VERIFIED BY A SUITABLY QUALIFIED PERSON BEFORE ANY USE FOR APPROVAL OR CONSTRUCTION. Not a survey. Not a development application drawing.
Cadastre, imagery and contours: NSW Spatial Services (CC BY). Aerial underlay: NSW Spatial Services (c) Department of Customer Service 2020. Sample picture only. Reduced resolution, not for measurement.

SITE PLAN 1:500 @ A3

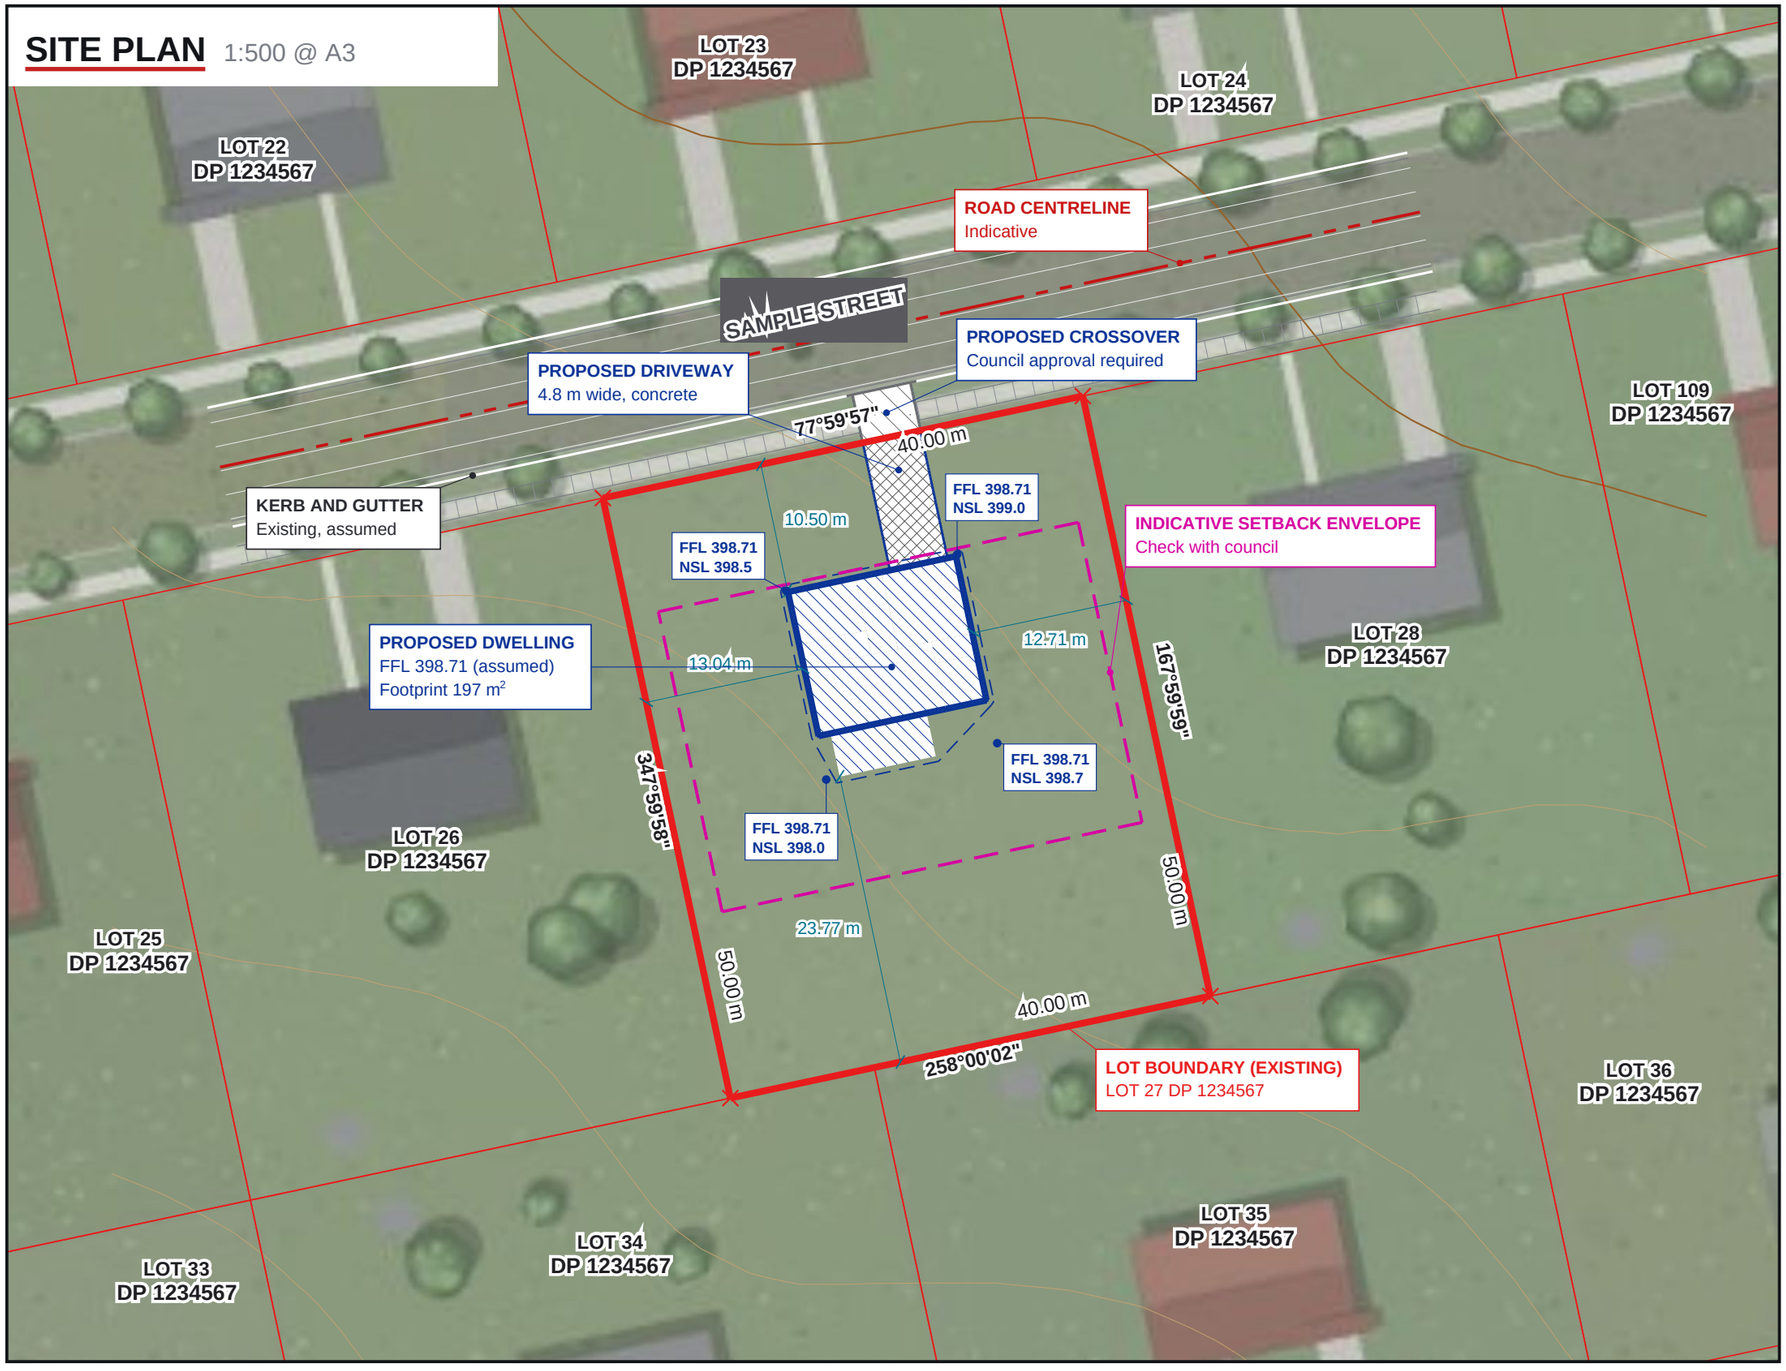

N


SCALE 1:500 @ A3

North is MGA grid north.

Plan up is north.

0 5 10 15 20 m

KEY PLAN

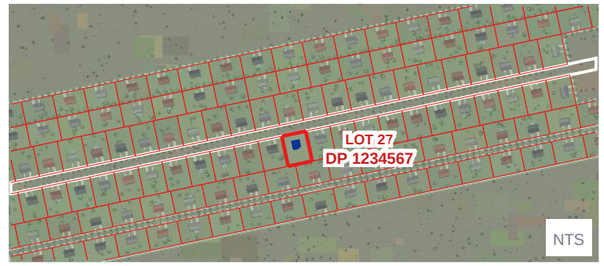

LEGEND

- Lot boundary (existing)
- Neighbouring lots (cadastre)
- Indicative setback envelope
- Road centreline (phantom, indicative)
- Kerb and gutter
- Contour (minor, major)
- Dimension to boundary
- Proposed works
- Hardstand (driveway)
- Concrete (crossover)
- Road pavement
- Footpath

NOTES

1. Concept only. To be verified by a suitably qualified person before any use for approval or construction.
2. Boundaries are from the cadastre, are indicative only, and are not a survey. A registered survey is required.
3. The aerial underlay is reduced in resolution and is for orientation only. It is not for measurement. Cadastre drawn in red over the aerial.
4. Setbacks are indicative (Tamworth Regional Council). The sources, the figures provided and the items to confirm are on sheet 8. A figure marked check with council is not confirmed.
5. Levels are indicative only, from the NSW 5 m DEM, and are not survey. Contours are at 1.0 m intervals and spot levels are to 0.1 m. A registered survey is required.
6. FFL 398.71 m AHD is assumed from the ground level at the house, not designed. NSL is the natural surface level from the terrain model at each house corner.

Glide Inside

Prepared with Glide Inside

PROJECT
SAMPLE RESIDENCE
14 SAMPLE STREET CALALA NSW
LOT 27 DP 1234567

CLIENT
A Sample Client

DRAWING TITLE
SITE PLAN

REV	DATE	DESCRIPTION	DRN	CHK	APP
A	11/11/2026	Concept			

NOT CHECKED. NOT APPROVED.

DRAWING NUMBER	REV	STATUS
GI-TAM24-A-002	A	CONCEPT

DATE	DRAWN	CHECKED	APPROVED	JOB NO.
11/11/2026				TAM24


SCALE	SHEET	SIZE
1:500 @ A3	2 OF 9	A3

CONCEPT ONLY. TO BE VERIFIED BY A SUITABLY QUALIFIED PERSON BEFORE ANY USE FOR APPROVAL OR CONSTRUCTION. Not a survey. Not a development application drawing.

Cadastre, imagery and contours: NSW Spatial Services (CC BY). Aerial underlay: NSW Spatial Services (c) Department of Customer Service 2020. Sample picture only. Reduced resolution, not for measurement.

NOTES

1. Dimensions are in millimetres, between wall faces as drawn. Wall construction is not designed here.
2. Floor level of this storey: RL 398.71 m AHD (assumed from the ground level at the house).
3. Ceiling height 2.55 m.
4. Section A-A is cut where the red chain line crosses the plan: see sheet 7.
5. Furniture is indicative and is not part of the design.

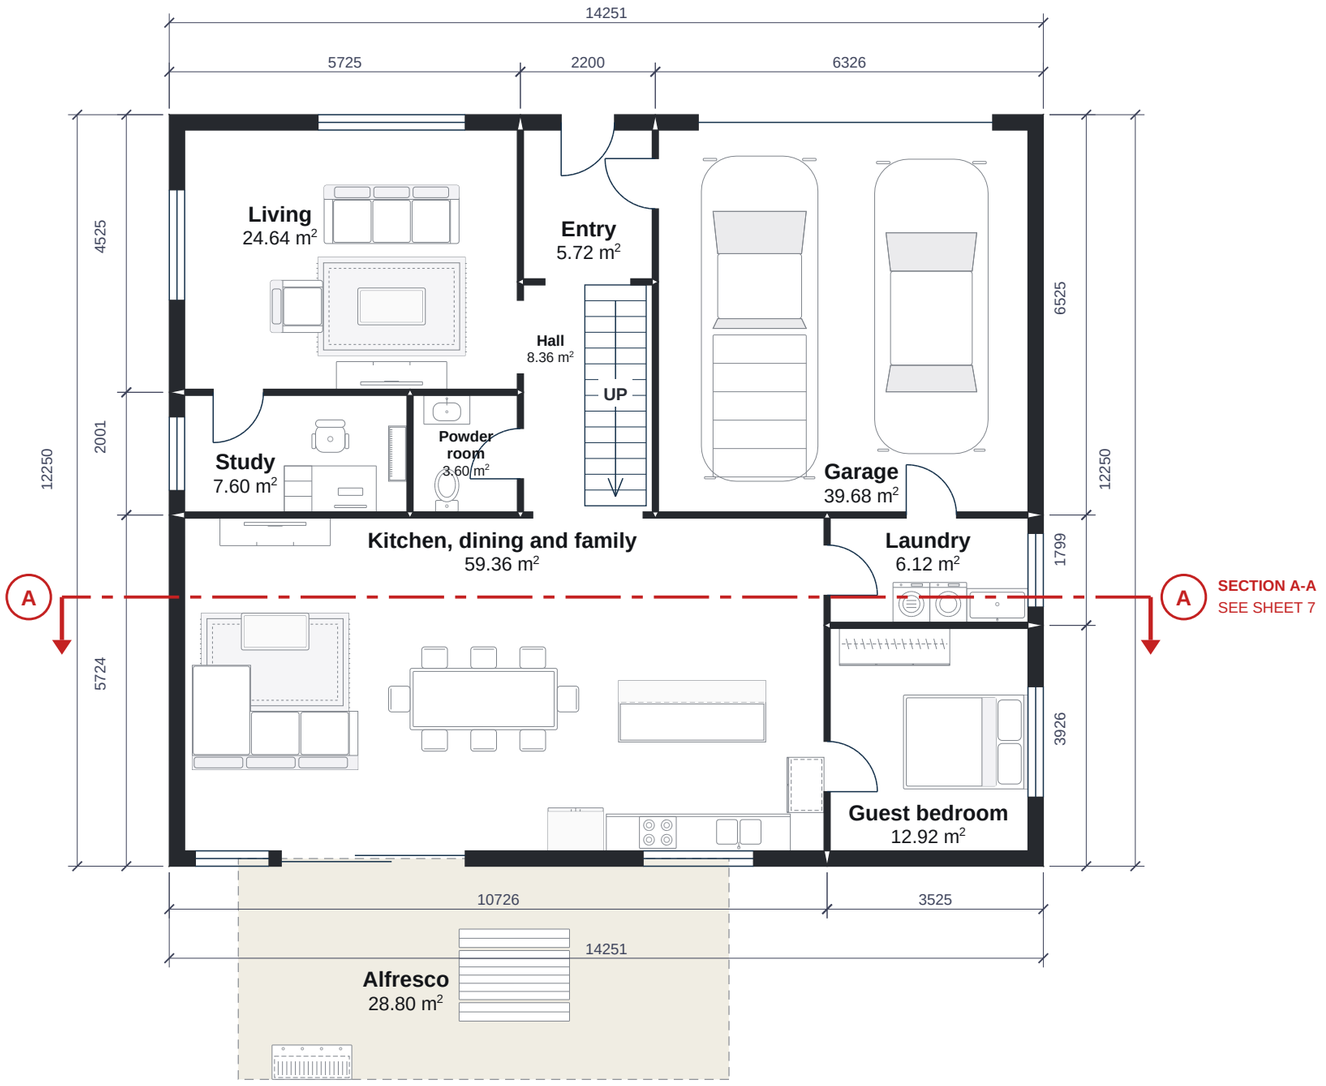

GROUND FLOOR PLAN

1:100 @ A3

0 1 2 3 4 5 m

N

Glide Inside

Prepared with Glide Inside

PROJECT
SAMPLE RESIDENCE
14 SAMPLE STREET CALALA NSW
LOT 27 DP 1234567

CLIENT
A Sample Client

DRAWING TITLE
GROUND FLOOR PLAN

REV	DATE	DESCRIPTION	DRN	CHK	APP
A	11/11/2026	Concept			

NOT CHECKED. NOT APPROVED.

DRAWING NUMBER	REV	STATUS
GI-TAM24-A-003	A	CONCEPT


DATE	DRAWN	CHECKED	APPROVED	JOB NO.
11/11/2026				TAM24

SCALE	SHEET	SIZE
1:100 @ A3	3 OF 9	A3

CONCEPT ONLY. TO BE VERIFIED BY A SUITABLY QUALIFIED PERSON BEFORE ANY USE FOR APPROVAL OR CONSTRUCTION. Not a survey. Not a development application drawing.
Cadastre, imagery and contours: NSW Spatial Services (CC BY). Aerial underlay: NSW Spatial Services (c) Department of Customer Service 2020. Sample picture only. Reduced resolution, not for measurement.

NOTES

1. Dimensions are in millimetres, between wall faces as drawn. Wall construction is not designed here.
2. Floor level of this storey: RL 401.71 m AHD (assumed from the ground level at the house).
3. Ceiling height 2.55 m.
4. Section A-A is cut where the red chain line crosses the plan: see sheet 7.
5. Furniture is indicative and is not part of the design.

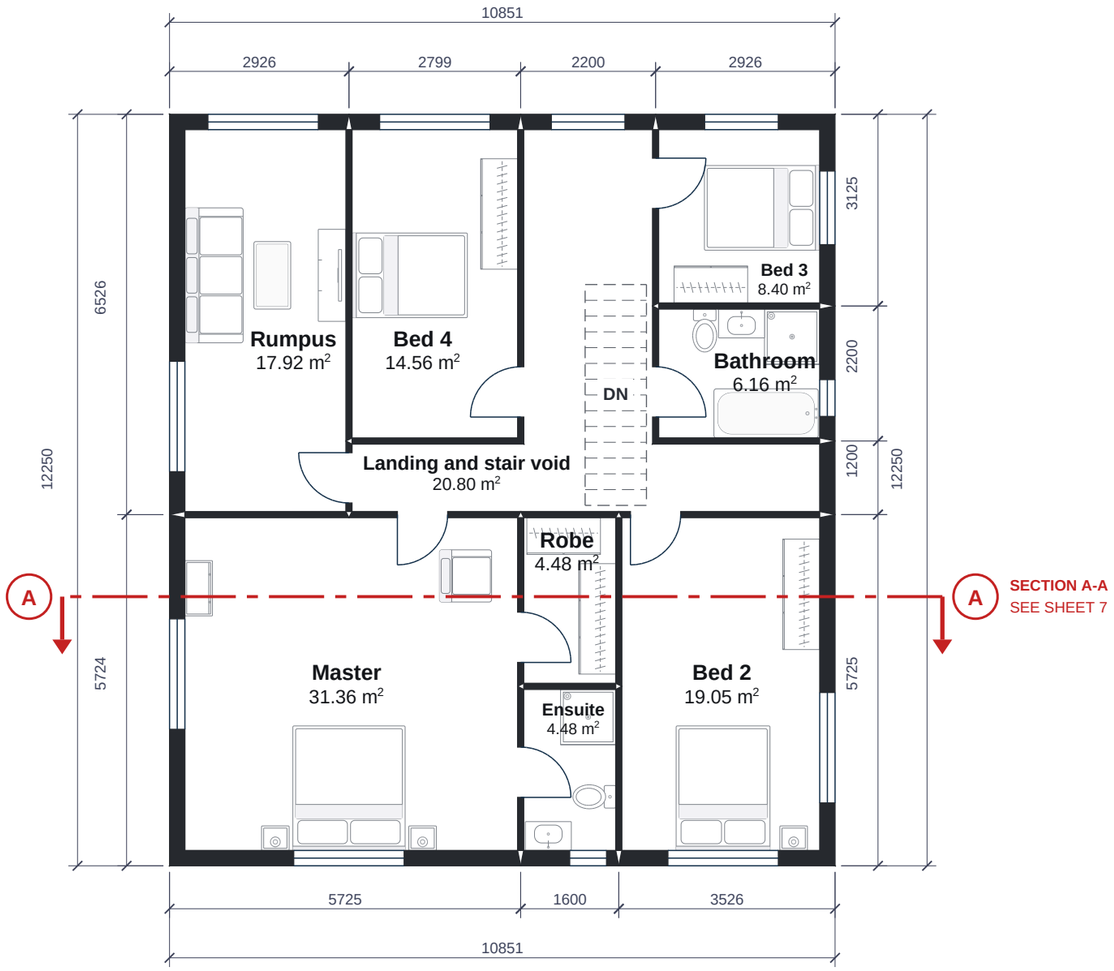

FIRST FLOOR PLAN

1:100 @ A3

0 1 2 3 4 5 m

N

Glide Inside

Prepared with Glide Inside

PROJECT
SAMPLE RESIDENCE
14 SAMPLE STREET CALALA NSW
LOT 27 DP 1234567

CLIENT
A Sample Client

DRAWING TITLE
FIRST FLOOR PLAN

REV	DATE	DESCRIPTION	DRN	CHK	APP
A	11/11/2026	Concept			

NOT CHECKED. NOT APPROVED.


DRAWING NUMBER	REV	STATUS
GI-TAM24-A-004	A	CONCEPT

DATE	DRAWN	CHECKED	APPROVED	JOB NO.
11/11/2026				TAM24

SCALE	SHEET	SIZE
1:100 @ A3	4 OF 9	A3

CONCEPT ONLY. TO BE VERIFIED BY A SUITABLY QUALIFIED PERSON BEFORE ANY USE FOR APPROVAL OR CONSTRUCTION. Not a survey. Not a development application drawing.
Cadastre, imagery and contours: NSW Spatial Services (CC BY). Aerial underlay: NSW Spatial Services (c) Department of Customer Service 2020. Sample picture only. Reduced resolution, not for measurement.

ROOF PLAN 1:100 @ A3

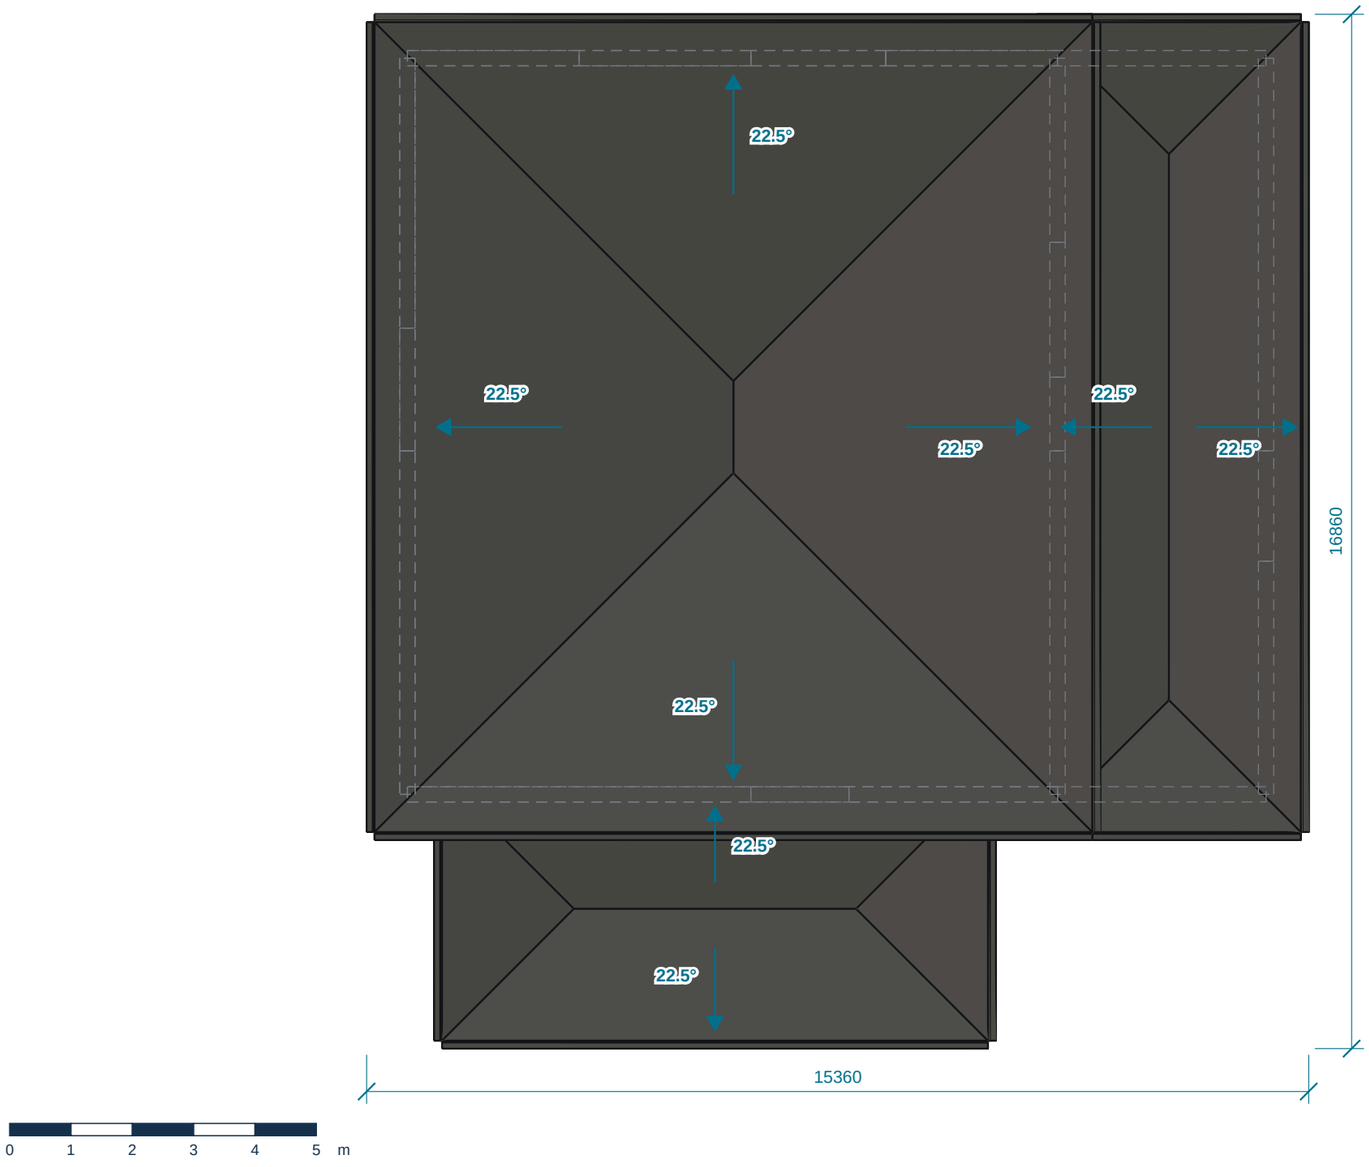

ROOF DATA

Roof form	**Hip roof**
Pitch	**22.5°**
Eaves overhang	**450 mm**
Roof area (sloped)	**335 m²**
Roof sheeting	**Not stated**
Highest point	**7.81 m above FFL, RL 406.52**
Above natural surface	**8.5 m at the lowest house corner**

LEGEND

- Ridge, hip and valley
- Direction of fall, with pitch
- Exterior walls below

Roof geometry is taken from the same model as the 3D view. Sheeting, gutters, downpipes, battens and roof framing are not designed here and are to be confirmed by the builder and a structural engineer. Dimensions are in millimetres.

Glide Inside

Prepared with Glide Inside

PROJECT
SAMPLE RESIDENCE
14 SAMPLE STREET CALALA NSW
LOT 27 DP 1234567

CLIENT
A Sample Client

DRAWING TITLE
ROOF PLAN

REV	DATE	DESCRIPTION	DRN	CHK	APP
A	11/11/2026	Concept			


NOT CHECKED. NOT APPROVED.

DRAWING NUMBER	REV	STATUS
GI-TAM24-A-005	**A**	**CONCEPT**

DATE	DRAWN	CHECKED	APPROVED	JOB NO.
11/11/2026				**TAM24**

SCALE	SHEET	SIZE
1:100 @ A3	**5 OF 9**	**A3**

CONCEPT ONLY. TO BE VERIFIED BY A SUITABLY QUALIFIED PERSON BEFORE ANY USE FOR APPROVAL OR CONSTRUCTION. Not a survey. Not a development application drawing.
Cadastre, imagery and contours: NSW Spatial Services (CC BY). Aerial underlay: NSW Spatial Services (c) Department of Customer Service 2020. Sample picture only. Reduced resolution, not for measurement.

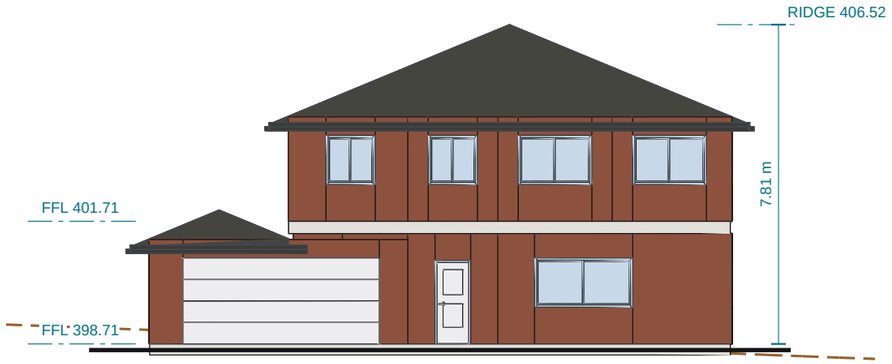


NORTH ELEVATION 1:150 @ A3



EAST ELEVATION 1:150 @ A3



SOUTH ELEVATION 1:150 @ A3

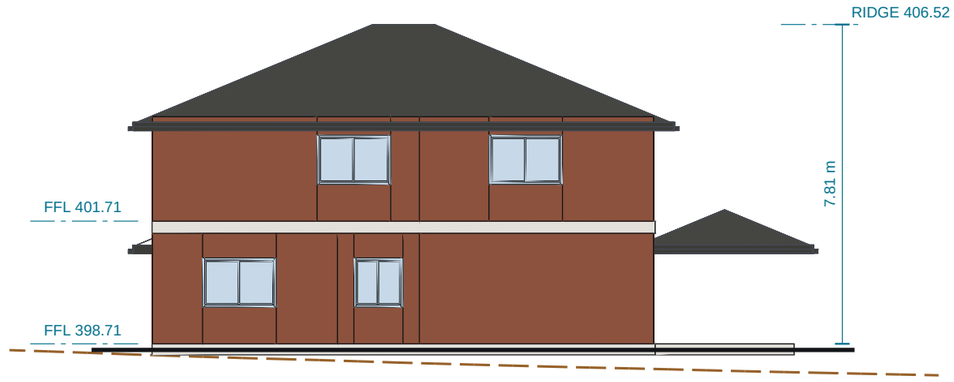

WEST ELEVATION 1:150 @ A3

Glide Inside

Prepared with Glide Inside

PROJECT
SAMPLE RESIDENCE
14 SAMPLE STREET CALALA NSW
LOT 27 DP 1234567

CLIENT
A Sample Client

DRAWING TITLE
ELEVATIONS

REV	DATE	DESCRIPTION	DRN	CHK	APP
A	11/11/2026	Concept			

NOT CHECKED. NOT APPROVED.

DRAWING NUMBER **GI-TAM24-A-006**
REV **A**
STATUS **CONCEPT**
DATE **11/11/2026**
DRAWN
CHECKED
APPROVED
JOB NO. **TAM24**
SCALE **1:150 @ A3**
SHEET **6 OF 9**
SIZE **A3**

CONCEPT ONLY. TO BE VERIFIED BY A SUITABLY QUALIFIED PERSON BEFORE ANY USE FOR APPROVAL OR CONSTRUCTION. Not a survey. Not a development application drawing.
Cadastre, imagery and contours: NSW Spatial Services (CC BY). Aerial underlay: NSW Spatial Services (c) Department of Customer Service 2020. Sample picture only. Reduced resolution, not for measurement.

SECTION A-A 1:50 @ A3

Cut across the centre of the house, looking south. Cut walls are hatched, slabs solid. The section line is marked on the floor plans.



Glide Inside

Prepared with Glide Inside

PROJECT
SAMPLE RESIDENCE
14 SAMPLE STREET CALALA NSW
LOT 27 DP 1234567

CLIENT
A Sample Client

DRAWING TITLE
SECTION


REV	DATE	DESCRIPTION	DRN	CHK	APP
A	11/11/2026	Concept			

NOT CHECKED. NOT APPROVED.

DRAWING NUMBER **GI-TAM24-A-007**
REV **A**
STATUS **CONCEPT**
DATE **11/11/2026**
DRAWN
CHECKED
APPROVED
JOB NO. **TAM24**
SCALE **1:50 @ A3**
SHEET **7 OF 9**
SIZE **A3**

CONCEPT ONLY. TO BE VERIFIED BY A SUITABLY QUALIFIED PERSON BEFORE ANY USE FOR APPROVAL OR CONSTRUCTION. Not a survey. Not a development application drawing.
Cadastre, imagery and contours: NSW Spatial Services (CC BY). Aerial underlay: NSW Spatial Services (c) Department of Customer Service 2020. Sample picture only. Reduced resolution, not for measurement.

SITE ANALYSIS 1:500 @ A3

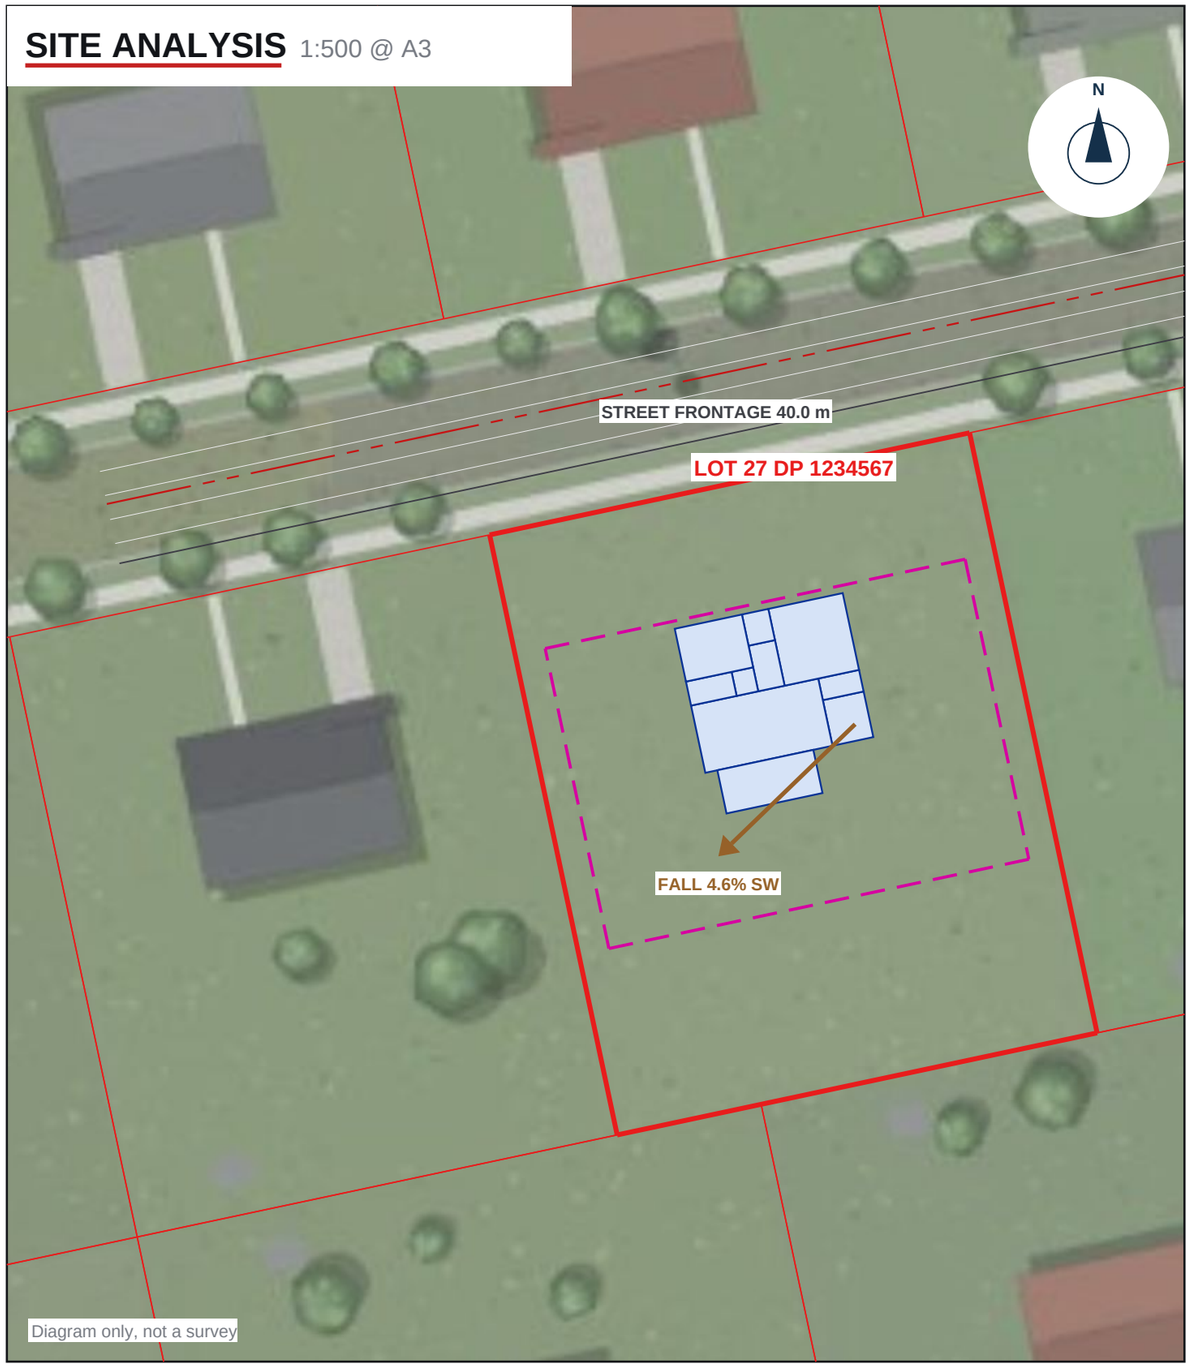

SITE FACTS

ITEM	DETAIL
Address	14 Sample Street Calala NSW
Lot and DP	LOT 27 DP 1234567
Council	Tamworth Regional
Zone	R5 Large Lot Residential
Site area	2000 m^2 (registered)
Frontage and depth	40.0 m by 50.0 m
Corner lot	No
Ground fall	2.76 m across the lot, 4.6% towards the SW
Floor level	FFL 398.71 m AHD (assumed)
Overlays	Bushfire, flood, heritage and easements not checked

SETBACKS: REQUIRED AND PROVIDED

BOUNDARY	REQUIRED	PROVIDED	RESULT	SOURCE AND CHECK
Front boundary	10.00 m	10.50 m	Inside the indicative setback envelope	Codes SEPP Inland Code primary road. Indicative. Check with council.
Side boundary 1	2.50 m	12.71 m	CHECK. Table minimum met. Parts over 4.5 m high need a larger side setback that is not captured.	Codes SEPP Inland Code side. Indicative. Check with council.
Rear boundary	15.00 m	23.77 m	Inside the indicative setback envelope	Codes SEPP Inland Code rear. Indicative. Check with council.
Side boundary 2	2.50 m	13.04 m	CHECK. Table minimum met. Parts over 4.5 m high need a larger side setback that is not captured.	Codes SEPP Inland Code side. Indicative. Check with council.

Rule set: Tamworth Regional Council, Codes SEPP Inland Code (complying development pathway; exclusions such as bushfire, flood and heritage apply). State Environmental Planning Policy (Exempt and Complying Development Codes) 2008, Part 3D Inland Code (as retrieved 11/11/2026; Indicative. Check with council.). Provided distances are the least distance from the building to each boundary, measured from the walls and rooms. A result here is not an approval.

ITEMS TO CONFIRM

ITEM	WHO CONFIRMS
Front: not yet confirmed with council	Council
Side: Table minimum shown. Parts of a building more than 4.5 m above ground need a larger side setback formula not captured)	Council
Rear: not yet confirmed with council	Council
Garage: not yet confirmed with council	Council
Bushfire attack level, flood, heritage and other overlays	Council or certifier
Easements, sewer and stormwater connection points, Before You Dig Australia plans	Surveyor and authorities
Registered survey: boundaries, levels, trees and existing structures	Registered surveyor
Crossover location, width and levels; driveway grade	Council
Structure, bracing and footings	Structural engineer

Glide Inside

Prepared with Glide Inside

PROJECT
SAMPLE RESIDENCE
14 SAMPLE STREET CALALA NSW
LOT 27 DP 1234567

CLIENT
A Sample Client

DRAWING TITLE
SITE ANALYSIS AND SETBACKS

REV	DATE	DESCRIPTION	DRN	CHK	APP
A	11/11/2026	Concept			

NOT CHECKED. NOT APPROVED.

DRAWING NUMBER **GI-TAM24-A-008** | REV **A** | STATUS **CONCEPT**

DATE **11/11/2026** | DRAWN | CHECKED | APPROVED | JOB NO. **TAM24**

SCALE **1:500 @ A3** | SHEET **8 OF 9** | SIZE **A3**

CONCEPT ONLY. TO BE VERIFIED BY A SUITABLY QUALIFIED PERSON BEFORE ANY USE FOR APPROVAL OR CONSTRUCTION. Not a survey. Not a development application drawing.
Cadastre, imagery and contours: NSW Spatial Services (CC BY). Aerial underlay: NSW Spatial Services (c) Department of Customer Service 2020. Sample picture only. Reduced resolution, not for measurement.

AREAS AND SITE COVERAGE

ITEM	AREA
Ground floor area	168.0 m²
First floor area	127.2 m²
Total internal floor area	**295.2 m²**
Outdoor areas	28.8 m²
Garage (included above)	39.7 m²
Building footprint (ground level)	196.8 m²
Site area	2000 m²
Site coverage (footprint over site area)	**9.8 %**
Roof area (from the model, sloped)	335.3 m²
Driveway within the lot (indicative)	51.0 m²
Crossover in the road reserve (indicative)	19.3 m²
Remaining site area (soft and other hard)	1752 m²

Areas are measured from the room polygons in the design. Site coverage uses the cadastre area unless a registered area is stated. Council definitions of floor area and coverage can differ: check with council.

SITE AREA BREAKDOWN



- Building footprint: 197 m² (10 %)
- Driveway within the lot: 51 m² (3 %)
- Remaining site area: 1752 m² (88 %)

ROOM SCHEDULE

LEVEL	ROOM	TYPE	M²
Ground	Guest bedroom	Bedroom	12.92
Ground	Laundry	Laundry	6.12
Ground	Kitchen, dining and family	Family	59.36
Ground	Garage	Garage	39.68
Ground	Hall	Hall	8.36
Ground	Entry	Entry	5.72
Ground	Powder room	WC	3.60
Ground	Study	Study	7.60
Ground	Living	Living	24.64
Ground	Alfresco	Alfresco	28.80
First	Bed 2	Bedroom	19.05
First	Ensuite	Ensuite	4.48
First	Robe	Robe	4.48
First	Master	Bedroom	31.36
First	Bathroom	Bathroom	6.16
First	Bed 3	Bedroom	8.40
First	Bed 4	Bedroom	14.56
First	Rumpus	Rumpus	17.92
First	Landing and stair void	Hall	20.80

19 rooms. Areas in square metres to two places.

DOOR AND WINDOW SCHEDULE

TYPE	W x H (MM)	SILL	QTY
Door	820 x 2040		12
Cavity door	820 x 2040		2
Door	870 x 2040		1
Garage door	4800 x 2100		1
Opening	1200 x 2040		1
Opening	1400 x 2040		1
Opening	1800 x 2040		1
Sliding door	3000 x 2100		1
Awning window	600 x 600	1500	2
Sliding window	1200 x 1200	900	5
Awning window	1200 x 600	1500	1
Sliding window	1800 x 900	1200	1
Sliding window	1800 x 1200	900	9
Sliding window	2400 x 1200	900	1

Total openings: 39

Colour scheme: Ironstone and Brick

Ironstone roof, Red Brick walls.

SCHEDULE NOTES

- Sizes are the nominal opening width and height in millimetres. The sill is the height of the sill above the finished floor level.
- Glazing, frame and hardware are to be selected by the builder. Window and door energy ratings, bushfire and wind rating requirements are not assessed here.
- Room names and types are those in the design. Areas are internal, measured to the face of the wall.

Glide Inside

Prepared with Glide Inside

PROJECT
SAMPLE RESIDENCE
14 SAMPLE STREET CALALA NSW
LOT 27 DP 1234567

CLIENT
A Sample Client

DRAWING TITLE
SCHEDULES

REV	DATE	DESCRIPTION	DRN	CHK	APP
A	11/11/2026	Concept			

NOT CHECKED. NOT APPROVED.

DRAWING NUMBER **GI-TAM24-A-009**
REV **A**
STATUS **CONCEPT**
DATE **11/11/2026**
DRAWN
CHECKED
APPROVED
JOB NO. **TAM24**
SCALE **NTS**
SHEET **9 OF 9**
SIZE **A3**

CONCEPT ONLY. TO BE VERIFIED BY A SUITABLY QUALIFIED PERSON BEFORE ANY USE FOR APPROVAL OR CONSTRUCTION. Not a survey. Not a development application drawing.
Cadastre, imagery and contours: NSW Spatial Services (CC BY). Aerial underlay: NSW Spatial Services (c) Department of Customer Service 2020. Sample picture only. Reduced resolution, not for measurement.