CONCEPT PLAN SET

MARSH RESIDENCE

Issue: Concept, revision A, 11/11/2026

DRAWING LIST

DRAWING NUMBER	TITLE	SCALE
GI-MARSHRES-A-001	Cover sheet and drawing list	AS SHOWN
GI-MARSHRES-A-002	Site plan	NTS
GI-MARSHRES-A-003	Ground floor plan	1:50 @ A3
GI-MARSHRES-A-004	Roof plan	1:50 @ A3
GI-MARSHRES-A-005	Elevations	1:100 @ A3
GI-MARSHRES-A-006	Section	1:50 @ A3
GI-MARSHRES-A-007	Site analysis and setbacks	NTS
GI-MARSHRES-A-008	Schedules	NTS

LOCALITY



This is a concept design for discussion. Setbacks, levels and boundaries are indicative and have not been checked by a surveyor, certifier or council. Where a council rule is marked check with council it has not been confirmed.

Prepared with Glide Inside

TRIAL · NOT FOR CONSTRUCTION OR LODGEMENT

Glide Inside

Prepared with Glide Inside

PROJECT
MARSH RESIDENCE

CLIENT

DRAWING TITLE
COVER SHEET AND DRAWING LIST

REV	DATE	DESCRIPTION	DRN	CHK	APP
A	11/11/2026	Concept			

NOT CHECKED. NOT APPROVED.

DRAWING NUMBER: GI-MARSHRES-A-001
REV: A
STATUS: CONCEPT
DATE: 11/11/2026
DRAWN:
CHECKED:
APPROVED:
JOB NO.:
SCALE: AS SHOWN
SHEET: 1 OF 8
SIZE: A3

CONCEPT ONLY. TO BE VERIFIED BY A SUITABLY QUALIFIED PERSON BEFORE ANY USE FOR APPROVAL OR CONSTRUCTION. Not a survey. Not a development application drawing.
Cadastre, imagery and contours: NSW Spatial Services (CC BY). Cadastre: Queensland Government (CC BY 4.0). Imagery and elevation: Queensland Government (CC BY-SA). Where used.

Free trial export from Glide Inside. Watermark removed once the account is active.

SITE PLAN NTS

NO LOT LOADED

Use Find my block to load the lot, its setbacks and ground levels. This sheet then shows the site plan.

TRIAL · NOT FOR CONSTRUCTION OR LODGEMENT

N

SCALE NTS

North is MGA grid north.

Plan up is north.

KEY PLAN

Locality not loaded

LEGEND

- Lot boundary (existing)
- Neighbouring lot boundary
- Indicative setback envelope
- Road centreline (phantom, indicative)
- Kerb and gutter
- Contour (minor, major)
- Dimension to boundary
- Proposed works
- Hardstand (driveway)
- Concrete (crossover)
- Road pavement
- Footpath

NOTES

1. Concept only. To be verified by a suitably qualified person before any use for approval or construction.
2. Boundaries are from the cadastre, are indicative only, and are not a survey. A registered survey is required.
3. Services, easements, trees, flood and bushfire overlays are not shown. Before You Dig Australia plans and a section 10.7 or equivalent certificate are required.
4. Driveway and crossover are indicative. Crossover location, width and levels need council approval.

Glide Inside

Prepared with Glide Inside

PROJECT: **MARSH RESIDENCE**

CLIENT:

DRAWING TITLE: **SITE PLAN**

REV	DATE	DESCRIPTION	DRN	CHK	APP
A	11/11/2026	Concept			

NOT CHECKED. NOT APPROVED.

DRAWING NUMBER: **GI-MARSHRES-A-002** | REV: **A** | STATUS: **CONCEPT**

DATE: **11/11/2026** | DRAWN: | CHECKED: | APPROVED: | JOB NO.:

SCALE: **NTS** | SHEET: **2 OF 8** | SIZE: **A3**


CONCEPT ONLY. TO BE VERIFIED BY A SUITABLY QUALIFIED PERSON BEFORE ANY USE FOR APPROVAL OR CONSTRUCTION. Not a survey. Not a development application drawing.

Cadastre, imagery and contours: NSW Spatial Services (CC BY). Cadastre: Queensland Government (CC BY 4.0). Imagery and elevation: Queensland Government (CC BY-SA). Where used.

Free trial export from Glide Inside. Watermark removed once the account is active.

NOTES

1. Dimensions are in millimetres, between wall faces as drawn. Wall construction is not designed here.
2. Floor level is not set: load the lot to give RLs.
3. Ceiling height 2.55 m.
4. Section A-A is cut where the red chain line crosses the plan: see sheet 6.
5. Furniture is indicative and is not part of the design.

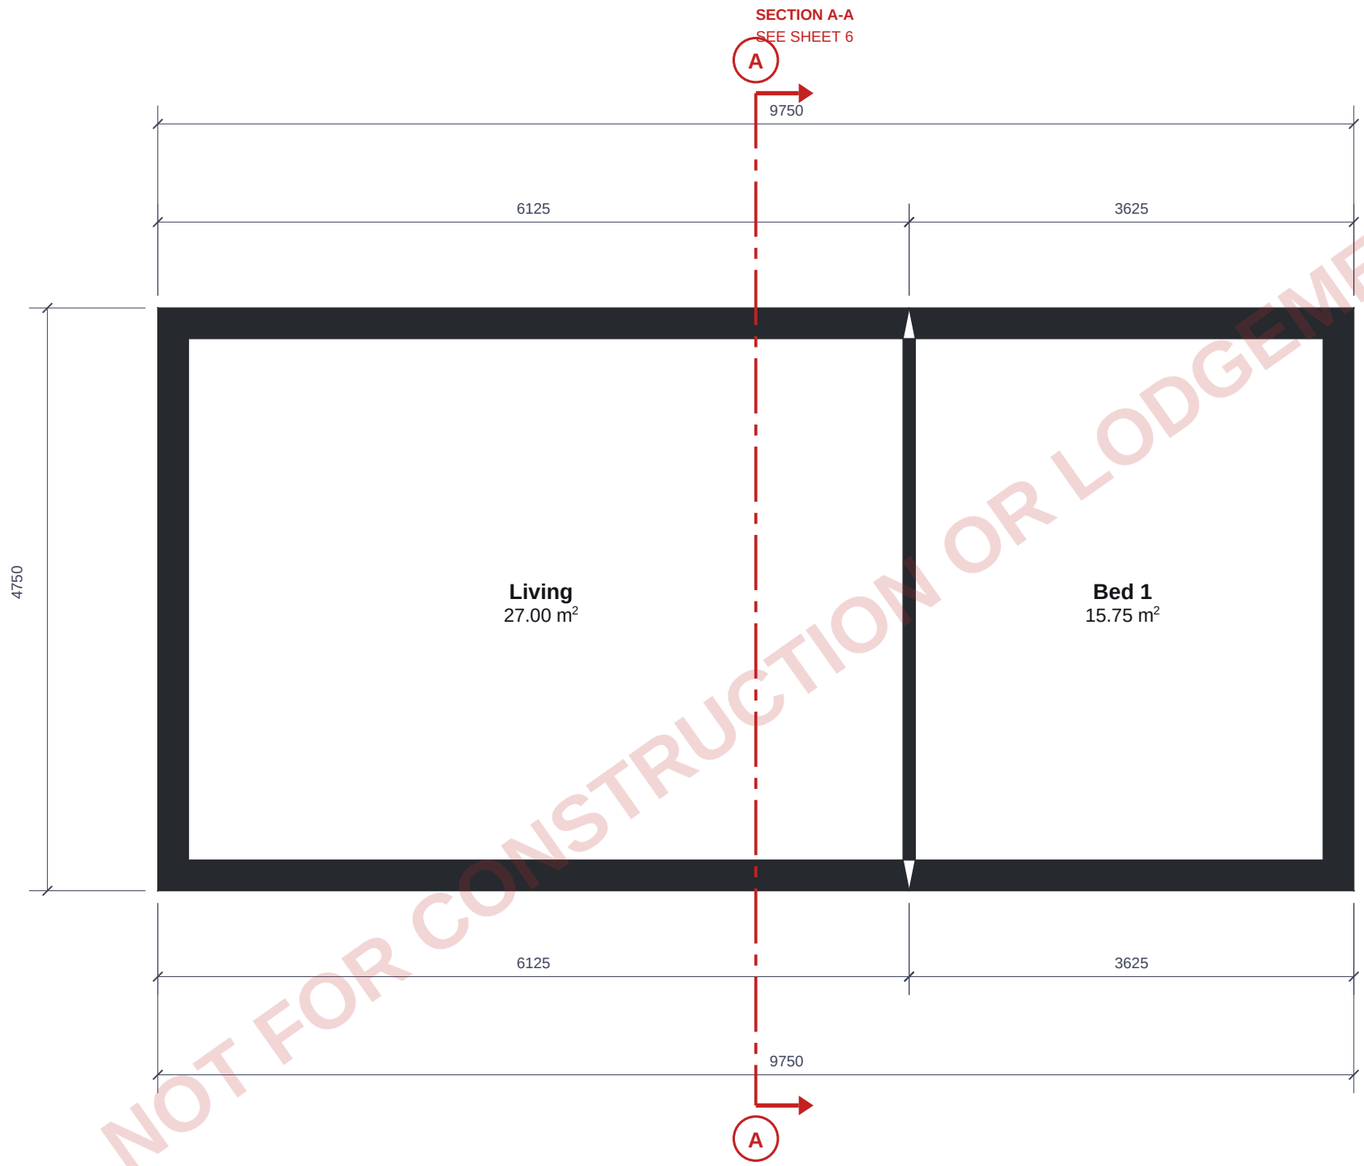

TRIAL · NOT FOR CONSTRUCTION OR LODGEMENT

GROUND FLOOR PLAN 1:50 @ A3

0 1 2 3 4 5 m

N

Glide Inside

Prepared with Glide Inside

PROJECT
MARSH RESIDENCE

CLIENT

DRAWING TITLE
GROUND FLOOR PLAN

REV	DATE	DESCRIPTION	DRN	CHK	APP
A	11/11/2026	Concept			

NOT CHECKED. NOT APPROVED.

DRAWING NUMBER	REV	STATUS
GI-MARSHRES-A-003	A	CONCEPT

DATE	DRAWN	CHECKED	APPROVED	JOB NO.
11/11/2026				


SCALE	SHEET	SIZE
1:50 @ A3	3 OF 8	A3

CONCEPT ONLY. TO BE VERIFIED BY A SUITABLY QUALIFIED PERSON BEFORE ANY USE FOR APPROVAL OR CONSTRUCTION. Not a survey. Not a development application drawing.

Cadastre, imagery and contours: NSW Spatial Services (CC BY). Cadastre: Queensland Government (CC BY 4.0). Imagery and elevation: Queensland Government (CC BY-SA). Where used.

Free trial export from Glide Inside. Watermark removed once the account is active.

ROOF PLAN 1:50 @ A3

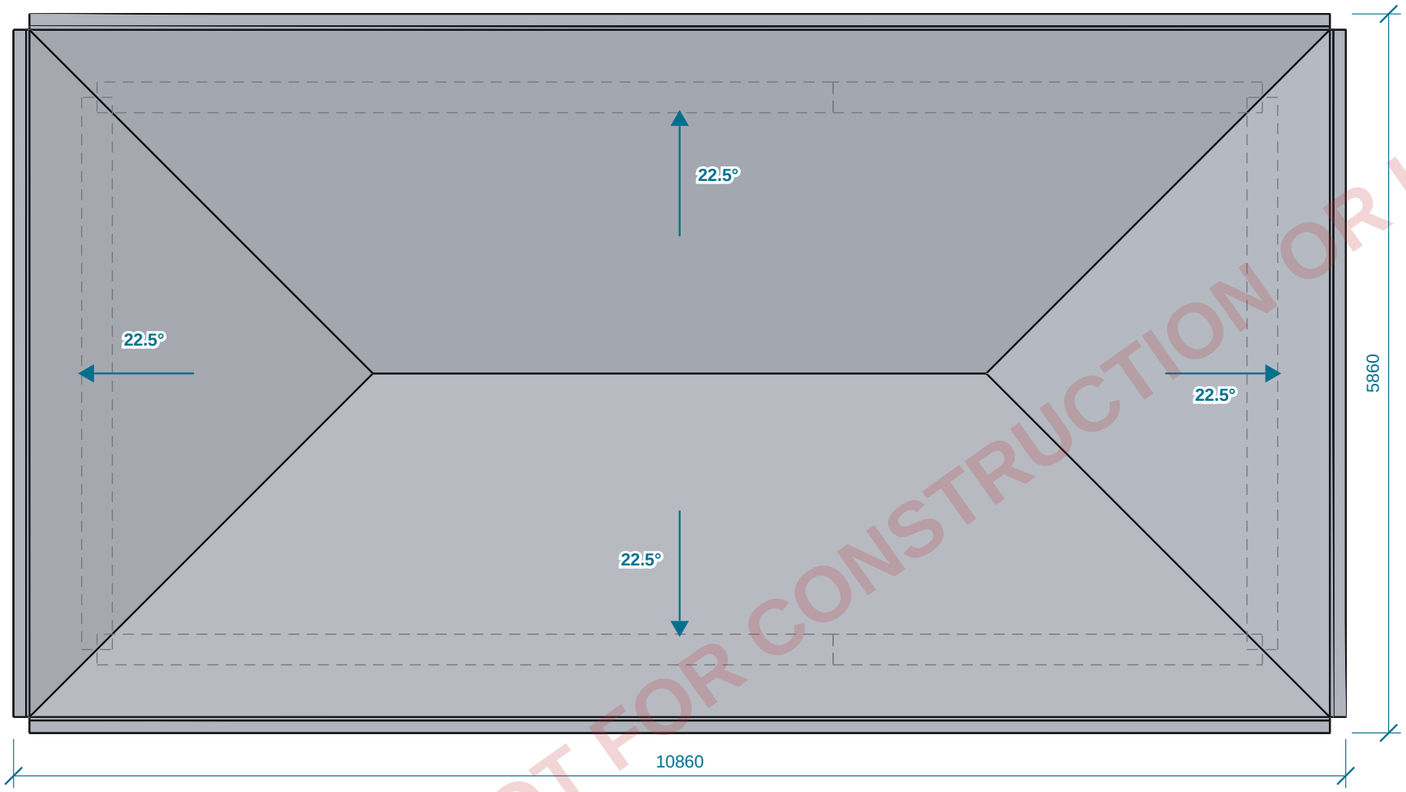

0 1 2 3 4 5 m

ROOF DATA

Roof form	**Hip roof**
Pitch	**22.5°**
Eaves overhang	**450 mm**
Roof area (sloped)	**92 m²**
Roof sheeting	**Not stated**
Highest point	**3.54 m above FFL**

LEGEND

- Ridge, hip and valley
- Direction of fall, with pitch
- Exterior walls below

Roof geometry is taken from the same model as the 3D view. Sheeting, gutters, downpipes, battens and roof framing are not designed here and are to be confirmed by the builder and a structural engineer. Dimensions are in millimetres.

TRIAL · NOT FOR CONSTRUCTION OR LODGEMENT

Glide Inside

Prepared with Glide Inside

PROJECT
MARSH RESIDENCE

CLIENT

DRAWING TITLE
ROOF PLAN


REV	DATE	DESCRIPTION	DRN	CHK	APP
A	11/11/2026	Concept			

NOT CHECKED. NOT APPROVED.


DRAWING NUMBER **GI-MARSHRES-A-004**
REV **A**
STATUS **CONCEPT**
DATE **11/11/2026**
DRAWN
CHECKED
APPROVED
JOB NO.
SCALE **1:50 @ A3**
SHEET **4 OF 8**
SIZE **A3**

CONCEPT ONLY. TO BE VERIFIED BY A SUITABLY QUALIFIED PERSON BEFORE ANY USE FOR APPROVAL OR CONSTRUCTION. Not a survey. Not a development application drawing.
Cadastre, imagery and contours: NSW Spatial Services (CC BY). Cadastre: Queensland Government (CC BY 4.0). Imagery and elevation: Queensland Government (CC BY-SA). Where used.


Free trial export from Glide Inside. Watermark removed once the account is active.

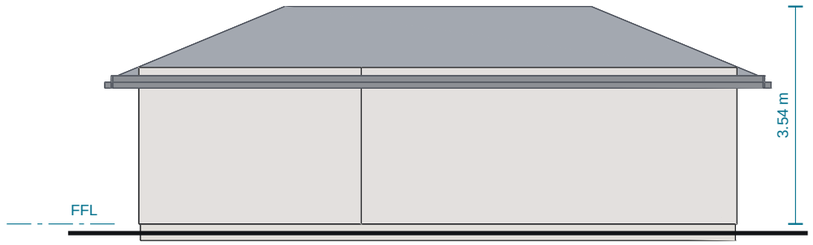


NORTH ELEVATION 1:100 @ A3

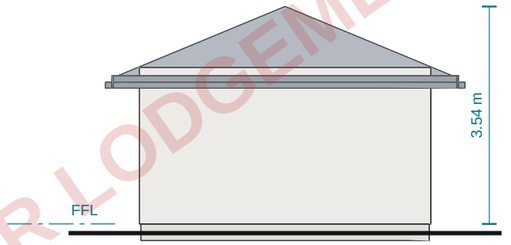

EAST ELEVATION 1:100 @ A3

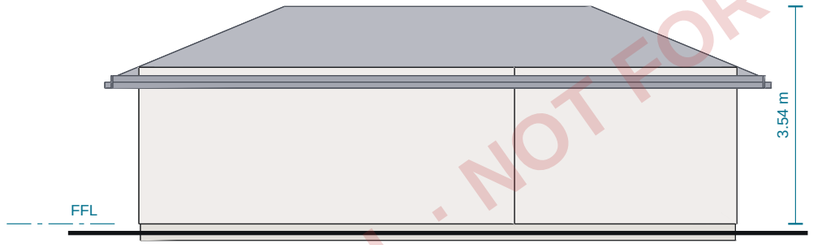

SOUTH ELEVATION 1:100 @ A3

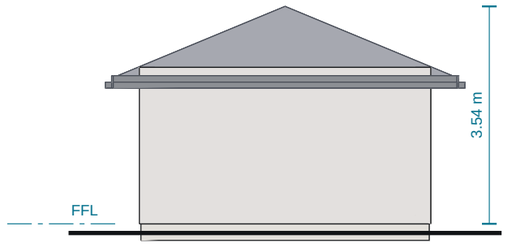

WEST ELEVATION 1:100 @ A3

TRIAL - NOT FOR CONSTRUCTION OR LODGEMENT

Glide Inside

Prepared with Glide Inside

PROJECT
MARSH RESIDENCE

CLIENT

DRAWING TITLE
ELEVATIONS

REV	DATE	DESCRIPTION	DRN	CHK	APP
A	11/11/2026	Concept			

NOT CHECKED. NOT APPROVED.


DRAWING NUMBER **GI-MARSHRES-A-005**
REV **A**
STATUS **CONCEPT**
DATE **11/11/2026**
DRAWN
CHECKED
APPROVED
JOB NO.
SCALE **1:100 @ A3**
SHEET **5 OF 8**
SIZE **A3**

CONCEPT ONLY. TO BE VERIFIED BY A SUITABLY QUALIFIED PERSON BEFORE ANY USE FOR APPROVAL OR CONSTRUCTION. Not a survey. Not a development application drawing.
Cadastre, imagery and contours: NSW Spatial Services (CC BY). Cadastre: Queensland Government (CC BY 4.0). Imagery and elevation: Queensland Government (CC BY-SA). Where used.

Free trial export from Glide Inside. Watermark removed once the account is active.

SECTION A-A 1:50 @ A3

Cut across the centre of the house, looking east. Cut walls are hatched, slabs solid. The section line is marked on the floor plans.

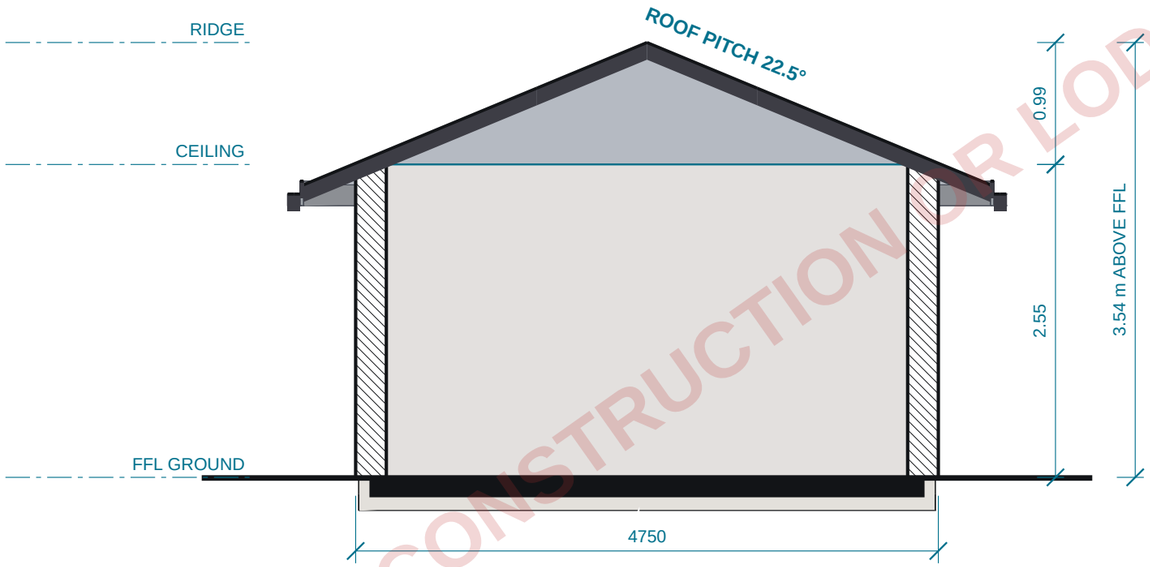



TRIAL · NOT FOR CONSTRUCTION OR LODGEMENT

Glide Inside

Prepared with Glide Inside

PROJECT
MARSH RESIDENCE

CLIENT

DRAWING TITLE
SECTION

REV	DATE	DESCRIPTION	DRN	CHK	APP
A	11/11/2026	Concept			

NOT CHECKED. NOT APPROVED.

DRAWING NUMBER **GI-MARSHRES-A-006**

REV **A**

STATUS **CONCEPT**

DATE	DRAWN	CHECKED	APPROVED	JOB NO.
11/11/2026				

SCALE	SHEET	SIZE
1:50 @ A3	6 OF 8	A3

CONCEPT ONLY. TO BE VERIFIED BY A SUITABLY QUALIFIED PERSON BEFORE ANY USE FOR APPROVAL OR CONSTRUCTION. Not a survey. Not a development application drawing.

Cadastre, imagery and contours: NSW Spatial Services (CC BY). Cadastre: Queensland Government (CC BY 4.0). Imagery and elevation: Queensland Government (CC BY-SA). Where used.

Free trial export from Glide Inside. Watermark removed once the account is active.

SETBACKS

No lot is loaded. Use Find my block to analyse the site.

TRIAL · NOT FOR CONSTRUCTION OR LODGEMENT

Glide Inside

Prepared with Glide Inside

PROJECT
MARSH RESIDENCE

CLIENT

DRAWING TITLE
SITE ANALYSIS AND SETBACKS

REV	DATE	DESCRIPTION	DRN	CHK	APP
A	11/11/2026	Concept			

NOT CHECKED. NOT APPROVED.

DRAWING NUMBER: **GI-MARSHRES-A-007**
REV: **A**
STATUS: **CONCEPT**
DATE: **11/11/2026**
DRAWN:
CHECKED:
APPROVED:
JOB NO.:
SCALE: **NTS**
SHEET: **7 OF 8**
SIZE: **A3**

CONCEPT ONLY. TO BE VERIFIED BY A SUITABLY QUALIFIED PERSON BEFORE ANY USE FOR APPROVAL OR CONSTRUCTION. Not a survey. Not a development application drawing.
Cadastre, imagery and contours: NSW Spatial Services (CC BY). Cadastre: Queensland Government (CC BY 4.0). Imagery and elevation: Queensland Government (CC BY-SA). Where used.

Free trial export from Glide Inside. Watermark removed once the account is active.

AREAS AND SITE COVERAGE

ITEM	AREA
Ground floor area	42.8 m²
Total internal floor area	**42.8 m²**
Building footprint (ground level)	42.8 m²
Roof area (from the model, sloped)	91.9 m²

Areas are measured from the room polygons in the design. Site coverage uses the cadastre area unless a registered area is stated. Council definitions of floor area and coverage can differ: check with council.

ROOM SCHEDULE

LEVEL	ROOM	TYPE	M²
Ground	Living	Living	27.00
Ground	Bed 1	Bedroom	15.75

2 rooms. Areas in square metres to two places.

DOOR AND WINDOW SCHEDULE

TYPE	W x H (MM)	SILL	QTY

Total openings: 0

SCHEDULE NOTES

- Sizes are the nominal opening width and height in millimetres. The sill is the height of the sill above the finished floor level.
- Glazing, frame and hardware are to be selected by the builder. Window and door energy ratings, bushfire and wind rating requirements are not assessed here.
- Room names and types are those in the design. Areas are internal, measured to the face of the wall.

TRIAL · NOT FOR CONSTRUCTION OR LODGEMENT

Glide Inside

Prepared with Glide Inside

PROJECT
MARSH RESIDENCE

CLIENT

DRAWING TITLE
SCHEDULES

REV	DATE	DESCRIPTION	DRN	CHK	APP
A	11/11/2026	Concept			

NOT CHECKED. NOT APPROVED.

DRAWING NUMBER
GI-MARSHRES-A-008

REV
A

STATUS
CONCEPT

DATE	DRAWN	CHECKED	APPROVED	JOB NO.
11/11/2026				

SCALE	SHEET	SIZE
NTS	8 OF 8	A3

CONCEPT ONLY. TO BE VERIFIED BY A SUITABLY QUALIFIED PERSON BEFORE ANY USE FOR APPROVAL OR CONSTRUCTION. Not a survey. Not a development application drawing.
Cadastre, imagery and contours: NSW Spatial Services (CC BY). Cadastre: Queensland Government (CC BY 4.0). Imagery and elevation: Queensland Government (CC BY-SA). Where used.

Free trial export from Glide Inside. Watermark removed once the account is active.